

Etat Descriptif de Division

Numéro de dossier : 2023-SNC-VILLE-ET-VIGNES-5402
Date de réalisation : 03/03/2023

**Résidence Ville et Vignes
25 Boulevard des Allées
69420 AMPUIS**



Objet :

Cet état descriptif de division a été établi selon le Décret n°55-1350 du 14 octobre 1955, pour l'application du décret n° 55-22 du 4 janvier 1955 portant réforme de la publicité foncière, modifié par Décret n°98-553 du 3 juillet 1998 - art. 30 JORF 4 juillet 1998.

L'état descriptif de division, prévu à l'article 7 du décret du 4 janvier 1955, peut être contenu soit dans un acte spécialement dressé à cet effet, soit dans un règlement de copropriété ou un cahier des charges concernant, en outre, l'organisation de la gestion collective, soit dans tout autre acte ou décision judiciaire. Un seul état descriptif doit être établi lorsque plusieurs bâtiments ou groupes de bâtiments pouvant faire l'objet de copropriétés particulières sont édifiés sur un sol dont la propriété est placée globalement sous le régime de l'indivision forcée.

A. - Désignation du ou des établissements

Localisation du ou des établissements :

Adresse (avec numéro de rue, voie) : ... **Résidence Ville et Vignes
25 Boulevard des Allées**

Département : **69420**

Commune (suivi du lieudit) : **AMPUIS**

Section cadastrale et parcelle : **Section cadastrale AB, Parcelles numéros 223, 637, 638 et 919**

Adresse de la copropriété : **Résidence Ville et Vignes
25 boulevard des Allées
69420 AMPUIS**

**B. - Désignation de l'exploitant**

Désignation de l'administration ou de l'exploitant :

Nom : **SNC VILLE ET VIGNES**
Adresse : **41 chemin du Colin 69370**
SAINT-DIDIER-AU-MONT-D'OR

Si l'exploitant n'est pas le donneur d'ordre : (sur déclaration de l'intéressé) :

Nom du donneur d'ordre : **URUS HABITAT**
Adresse : **1 rue Childebert**
69002 LYON

C. - Désignation de la personne ayant réalisé cet état descriptif de division

Nom et prénom : **PERRENOT Frédéric**
Raison sociale et nom de l'entreprise : **FPE EXPERTISE**
Adresse : **189 Chemin des Grandes Bruyères**
38121 CHONAS L'AMBALLAN
Numéro SIRET : **501 662 316 00014**
Désignation de la compagnie d'assurance : ... **MAVIT**
Numéro de police et date de validité : **2011852 - 31/12/2023**

D. - Description générale de l'immeuble :**Descriptif de la copropriété :**

L'ensemble immobilier, objet des présentes, est composé de 2 bâtiments.

Le bâtiment 1 à usage d'habitation, de commerces et de bureaux est édifié sur 4 niveaux.
Les étages sont desservis par un escalier A et un ascenseur.

Le bâtiment 2 à usage d'habitation avec garages et emplacements de stationnement est édifié sur 3 niveaux.
Les étages côté nord sont desservis par un escalier B et un ascenseur.
Les étages côté sud sont desservis par un escalier C.

On accède à cet ensemble immobilier par le n° 25 boulevard des Allées.

Délimitation de la copropriété :

Au nord, le boulevard des Allées.

Au sud, une parcelle cadastrée section AB n° 744 donnant sur une voie ferrée.

A l'est, un ensemble immobilier, parcelle cadastrée section AB n° 220.

A l'ouest, un ensemble immobilier, parcelle cadastrée section AB n° 224 et parcelle cadastrée AB n° 225, une parcelle cadastrée section AB n° 639 et l'avenue de la Gare.





Composition de la copropriété :

Bâtiment 1 :

Au rez-de-jardin : 2 bureaux.
 Au rez-de-chaussée : hall d'entrée et 2 locaux commerciaux.
 Au 1^{er} étage : palier et 4 appartements dont 2 duplex.
 Au 2^{ème} étage : palier et 4 appartements dont 2 duplex.

Bâtiment 2 :

Au rez-de-jardin : 2 halls d'entrée, 2 appartements, 7 garages dont 2 en accessibilité PMR.
 Au 1^{er} étage : 2 paliers et 4 appartements dont 2 duplex.
 Au 2^{ème} étage : 2 paliers et 4 appartements dont 2 duplex.

La copropriété comprend 19 emplacements de parkings privatifs en rez-de-jardin, dont 1 en accessibilité PMR (parkings n° 1, 2, 4 à 7 et 10 à 22).

La copropriété comprend 3 emplacements de parkings communs en rez-de-jardin, dont 1 en accessibilité PMR (parkings n° 3, 8 et 9).

E. - Hypothèses de calcul utilisées :

Article 76 de la loi SRU du 13 Décembre 2000 :

Mode de calcul des quotes-parts de parties communes et de la répartition des charges de copropriété.

L'article 10 de la loi n° 65-557 du 10 Juillet 1965 précitée est complété par un alinéa ainsi rédigé :

« Tout règlement de copropriété publié à compter du 31 décembre 2002 indique les éléments pris en considération et la méthode de calcul permettant de fixer les quotes-parts de parties communes et la répartition des charges »

Méthodologie :

Est adoptée pour le calcul des tantièmes de copropriété, la méthode préconisée par l'article 5 de la loi du 10 juillet 1965. Bien que cette méthode ne soit pas d'ordre public, elle a été suivie ; cela présente l'avantage de pouvoir utiliser ensuite les tantièmes de copropriété affectés à chaque lot comme base de répartition des charges relatives à la conservation, à l'entretien et à l'administration de l'immeuble.

Cette position adoptée, les solutions suivantes ont été dégagées à propos de l'appréciation de la superficie, de la consistance et la situation des lots.

Superficie privative des lots :

La superficie retenue pour les calculs de tantièmes correspond à une surface de plancher utile entre cloisons, appréciée au moment de l'établissement de la copropriété. Elle répond, à l'article 46 de la loi n°65 - 557 du 10 juillet 1965, telle qu'elle est définie par le décret en Conseil d'Etat prévu à l'article 47. (Selon les prescriptions de la loi CARREZ du 18.12.1996). Cette superficie comprend également les superficies annexes qui seront pondérées selon la consistance. Elle ne pourra, donc, pas être utilisée, sans vérification préalable, pour la rédaction d'attestation de superficie, notamment.

Consistance des lots :

Consistance selon les éléments suivants :

- Nature du lot.
- Distribution et forme.
- Hauteur sous plafond.

Pour le calcul des tantièmes, il a été utilisé la superficie de chaque lot pondérée par les coefficients suivants :

Nature des Lots	Coefficient de pondération
Cave	0,35
Grenier	0,4
Garage	0,6
Parking couvert	0,3
Parking ouvert	0,1
Jardin privé	0,2
Balcon	0,4
Terrasse	0,4
Appartement	1
Local commercial	1
Bureau	1

Activités	Coefficient de pondération
Commerce	2
Appartement	1
Formation	3
Bureau	2



Etage, ascenseur, escalier	Coefficient avec ascenseur	Coefficient sans ascenseur	Coefficient ascenseur	Coefficient escalier
Sous-sol	1	1	1,15	1,1
Rez-de-jardin	1	1	1	1
Rez-de-chaussée	1	1	1	1
1er étage	1,02	1,02	1	1
2ème étage	1,04	1,04	1,15	1,1
3ème étage	1,06	1,06	1,3	1,2
4ème étage	1,08	1	1,45	1,3
5ème étage	1,1	0,9	1,6	1,4
6ème étage	1,12	0,8	1,7	1,5
7ème étage	1,12	0,6	1,7	1,6
8ème étage	1,12	0,6	1,7	1,7
9ème étage	1,12	0,6	1,7	1,7
10ème étage	1,12	0,6	1,7	1,7
11ème étage	1,12	0,6	1,7	1,7
12ème étage	1,12	0,6	1,7	1,7
13ème étage	1,12	0,6	1,7	1,7
14ème étage	1,12	0,6	1,7	1,7
15ème étage	1,12	0,6	1,7	1,7
16ème étage	1,12	0,6	1,7	1,7
17ème étage	1,12	0,6	1,7	1,7
18ème étage	1,12	0,6	1,7	1,7
19ème étage	1,12	0,6	1,7	1,7
20ème étage	1,12	0,6	1,7	1,7

Hauteurs sous plafond	Coefficient de pondération
> 3,20 m	1,15
3,10 m	1,13
3 m	1,11
2,90 m	1,09
2,80 m	1,07
2,70 m	1,05
2,60 m	1,03
2,50 m	1
2,40 m	0,95
2,30 m	0,9
2,20 m	0,85
2,10 m	0,8
2 m	0,75
1,90 m	0,7
1,80 m	0,65
1,70 m	0,6
1,60 m	0,55
< 1,60 m	0,5

Eclaircissement	Coefficient de pondération
Nord	0,96
Sud	1
Est	0,98
Ouest	0,98

Vue	Coefficient de pondération
Dégagée	1
Masquée	0,96

Chauffage/Climatisation	Coefficient de pondération
Sans Objet	-
ECS	Coefficient de pondération
Sans Objet	-
ENR	Coefficient de pondération
Sans Objet	-

L'application de ces coefficients en utilisant une méthode de moyenne géométrique a permis de définir la superficie pondérée de chaque lot.

Les tantièmes rapportés à **10 000** ont été déterminés en appliquant une règle de trois.

Formules de calcul utilisées :

Surface pour chaque lot :

(Coef_Surface + Coef_Nature + Coef_Activite + Coef_HSP + Coef_Vue + Coef_Eclaircissement)) / Nb de coefficients différents de 0

Escalier pour chaque lot :

Coef_Surface x Coef_Nature x Coef_Activite x Coef_Escalier

Ascenseur pour chaque lot :

Coef_Surface x Coef_Nature x Coef_Activite x Coef_Ascenseur

ECS pour chaque lot :

Coef_Surface x Coef_Nature x Coef_Activite x Coef_ECS

Chauffage / climatisation pour chaque lot :

Coef_Surface x Coef_Nature x Coef_Activite x Coef_ChauffageClim

EnR pour chaque lot :

Coef_Surface x Coef_Nature x Coef_Activite x Coef_EnR

Critère 1 pour chaque lot :

Coef_Surface x Coef_Nature x Coef_Activite x Coef_Critere1

Critère 2 pour chaque lot :

Coef_Surface x Coef_Nature x Coef_Activite x Coef_Critere2

Critère 3 pour chaque lot :

Coef_Surface x Coef_Nature x Coef_Activite x Coef_Critere3

Critère 4 pour chaque lot :

Coef_Surface x Coef_Nature x Coef_Activite x Coef_Critere4

F. - Descriptifs des lots :**Bâtiment 1****Description du lot dénommé : Lot 1** (situé au Rez-de-jardin)

Descriptif : Bureaux en rez-de-jardin du bâtiment 1, comprenant : 3 pièces en plateau.

Accès direct par l'extérieur côté sud du bâtiment.

Il correspond aux 1135/10000° de la quote-part de l'immeuble Bâtiment 1

Il correspond aux 798/10000° de la quote-part de l'ensemble immobilier

Il correspond aux 0/10000° de la quote-part des charges d'ascenseur de l'immeuble Bâtiment 1

Il correspond aux 0/10000° de la quote-part des charges d'escalier de l'immeuble Bâtiment 1

Description du lot dénommé : Lot 2 (situé au Rez-de-jardin)

Descriptif : Bureaux en rez-de-jardin du bâtiment 1, comprenant : 2 pièces en plateau.

Accès direct par l'extérieur côté sud du bâtiment.

Il correspond aux 1183/10000° de la quote-part de l'immeuble Bâtiment 1

Il correspond aux 832/10000° de la quote-part de l'ensemble immobilier

Il correspond aux 0/10000° de la quote-part des charges d'ascenseur de l'immeuble Bâtiment 1

Il correspond aux 0/10000° de la quote-part des charges d'escalier de l'immeuble Bâtiment 1

Description du lot dénommé : Lot 3 (situé au Rez-de-chaussée)

Descriptif : Local commercial au rez-de-chaussée du bâtiment 1, comprenant : 2 pièces en plateau.

Accès direct par l'extérieur depuis le boulevard des Allées.

Il correspond aux 1962/10000° de la quote-part de l'immeuble Bâtiment 1

Il correspond aux 1379/10000° de la quote-part de l'ensemble immobilier

Il correspond aux 0/10000° de la quote-part des charges d'ascenseur de l'immeuble Bâtiment 1

Il correspond aux 0/10000° de la quote-part des charges d'escalier de l'immeuble Bâtiment 1

Description du lot dénommé : Lot 4 (situé au Rez-de-chaussée)

Descriptif : Local commercial au rez-de-chaussée du bâtiment 1, comprenant : 2 pièces en plateau.

Accès direct par l'extérieur depuis le boulevard des Allées.

Il correspond aux 2134/10000° de la quote-part de l'immeuble Bâtiment 1

Il correspond aux 1499/10000° de la quote-part de l'ensemble immobilier

Il correspond aux 0/10000° de la quote-part des charges d'ascenseur de l'immeuble Bâtiment 1

Il correspond aux 0/10000° de la quote-part des charges d'escalier de l'immeuble Bâtiment 1

Description du lot dénommé : Lot 5 (situé au 1er étage)

Descriptif : Appartement T2 au 1er étage du bâtiment 1, comprenant : entrée, WC, séjour/cuisine, chambre, salle de bains et balcon.

Accès par l'escalier A depuis la porte gauche sur le palier.

Il correspond aux 274/10000° de la quote-part de l'immeuble Bâtiment 1

Il correspond aux 192/10000° de la quote-part de l'ensemble immobilier

Il correspond aux 617/10000° de la quote-part des charges d'ascenseur de l'immeuble Bâtiment 1

Il correspond aux 643/10000° de la quote-part des charges d'escalier de l'immeuble Bâtiment 1

**Description du lot dénommé : Lot 6** (situé au 1er étage)

Descriptif : Appartement T2 au 1er étage du bâtiment 1, comprenant : entrée, séjour/cuisine, dégagement, chambre, WC, salle de bains et balcon.

Accès par l'escalier A depuis la porte au fond du couloir sur le palier.

Il correspond aux 320/10000° de la quote-part de l'immeuble Bâtiment 1

Il correspond aux 225/10000° de la quote-part de l'ensemble immobilier

Il correspond aux 720/10000° de la quote-part des charges d'ascenseur de l'immeuble Bâtiment 1

Il correspond aux 750/10000° de la quote-part des charges d'escalier de l'immeuble Bâtiment 1

Description du lot dénommé : Lot 7 (situé au 1er étage)

Descriptif : Appartement T2 Bis au 1er étage du bâtiment 1, comprenant : entrée, dégagement, WC, cuisine, chambre, séjour, salle de bains et terrasse.

Accès par l'escalier A depuis la 2ème porte droite sur le palier.

Il correspond aux 433/10000° de la quote-part de l'immeuble Bâtiment 1

Il correspond aux 304/10000° de la quote-part de l'ensemble immobilier

Il correspond aux 936/10000° de la quote-part des charges d'ascenseur de l'immeuble Bâtiment 1

Il correspond aux 975/10000° de la quote-part des charges d'escalier de l'immeuble Bâtiment 1

Description du lot dénommé : Lot 8 (situé au 1er étage)

Descriptif : Appartement T4 au 1er étage du bâtiment 1, comprenant : entrée, WC, séjour/cuisine, dégagement, 3 chambres, salle de bains, salle d'eau et terrasse.

Accès par l'escalier A depuis la 1ère porte droite sur le palier.

Il correspond aux 545/10000° de la quote-part de l'immeuble Bâtiment 1

Il correspond aux 383/10000° de la quote-part de l'ensemble immobilier

Il correspond aux 1180/10000° de la quote-part des charges d'ascenseur de l'immeuble Bâtiment 1

Il correspond aux 1228/10000° de la quote-part des charges d'escalier de l'immeuble Bâtiment 1

Description du lot dénommé : Lot 9 (situé au 2ème étage, 3ème étage)

Descriptif : Appartement T3 duplex au 2ème étage du bâtiment 1, comprenant au R+2 : entrée, WC, séjour/cuisine, cellier et balcon ; au R+3 : dégagement, salle de bains, 2 chambres et espaces rangement avec hauteur sous plafond < 1.80 m.

Accès par l'escalier A depuis la porte gauche sur le palier.

Il correspond aux 453/10000° de la quote-part de l'immeuble Bâtiment 1

Il correspond aux 318/10000° de la quote-part de l'ensemble immobilier

Il correspond aux 1475/10000° de la quote-part des charges d'ascenseur de l'immeuble Bâtiment 1

Il correspond aux 1442/10000° de la quote-part des charges d'escalier de l'immeuble Bâtiment 1

Description du lot dénommé : Lot 10 (situé au 2ème étage, 3ème étage)

Descriptif : Appartement T2 duplex au 2ème étage du bâtiment 1, comprenant au R+2 : entrée, WC, séjour/cuisine et balcon ; au R+3 : dégagement, salle de bains, chambre et espaces rangement avec hauteur sous plafond < 1.80 m.

Accès par l'escalier A depuis la porte au fond du couloir sur le palier.

Il correspond aux 415/10000° de la quote-part de l'immeuble Bâtiment 1

Il correspond aux 291/10000° de la quote-part de l'ensemble immobilier

Il correspond aux 1377/10000° de la quote-part des charges d'ascenseur de l'immeuble Bâtiment 1

Il correspond aux 1347/10000° de la quote-part des charges d'escalier de l'immeuble Bâtiment 1

Description du lot dénommé : Lot 11 (situé au 2ème étage, 3ème étage)

Descriptif : Appartement T3 duplex au 2ème étage du bâtiment 1, comprenant au R+2 : entrée, dégagement, séjour/cuisine, salle de bains, WC, chambre et balcon ; au R+3 : dégagement, salle d'eau, chambre et espaces rangement avec hauteur sous plafond < 1.80 m.

Accès par l'escalier A depuis la 2ème porte droite sur le palier.

Il correspond aux 519/10000° de la quote-part de l'immeuble Bâtiment 1

Il correspond aux 364/10000° de la quote-part de l'ensemble immobilier

Il correspond aux 1703/10000° de la quote-part des charges d'ascenseur de l'immeuble Bâtiment 1

Il correspond aux 1666/10000° de la quote-part des charges d'escalier de l'immeuble Bâtiment 1

Description du lot dénommé : Lot 12 (situé au 2ème étage, 3ème étage)

Descriptif : Appartement T4 duplex au 2ème étage du bâtiment 1, comprenant au R+2 : entrée, séjour/cuisine, dégagement, WC, chambre et balcon ; au R+3 : dégagement, salle de bains, 2 chambres et espaces rangement avec hauteur sous plafond < 1.80 m.

Accès par l'escalier A depuis la 1ère porte droite sur le palier.

Il correspond aux 627/10000° de la quote-part de l'immeuble Bâtiment 1

Il correspond aux 440/10000° de la quote-part de l'ensemble immobilier

Il correspond aux 1992/10000° de la quote-part des charges d'ascenseur de l'immeuble Bâtiment 1

Il correspond aux 1949/10000° de la quote-part des charges d'escalier de l'immeuble Bâtiment 1

**Bâtiment 2****Description du lot dénommé : Lot 13** (situé au Rez-de-jardin)

Descriptif : Appartement T3 au rez-de-jardin du bâtiment 2, comprenant : entrée, WC, séjour/cuisine, dégagement, salle de bains, 2 chambres, terrasse et jardin privatif.

Accès par l'escalier C depuis la porte unique du hall d'entrée.

Il correspond aux 1065/10000° de la quote-part de l'immeuble Bâtiment 2

Il correspond aux 307/10000° de la quote-part de l'ensemble immobilier

Il correspond aux 0/10000° de la quote-part des charges d'ascenseur de l'immeuble Bâtiment 2

Il correspond aux 0/10000° de la quote-part des charges d'escalier de l'immeuble Bâtiment 2

Description du lot dénommé : Lot 14 (situé au Rez-de-jardin)

Descriptif : Appartement T3 au rez-de-jardin du bâtiment 2, comprenant : entrée, séjour/cuisine, cellier, WC, salle de bains, 2 chambres, terrasse et jardin privatif.

Accès par l'escalier B depuis la porte unique du hall d'entrée.

Il correspond aux 1077/10000° de la quote-part de l'immeuble Bâtiment 2

Il correspond aux 310/10000° de la quote-part de l'ensemble immobilier

Il correspond aux 0/10000° de la quote-part des charges d'ascenseur de l'immeuble Bâtiment 2

Il correspond aux 0/10000° de la quote-part des charges d'escalier de l'immeuble Bâtiment 2

Description du lot dénommé : Lot 15 (situé au 1er étage, 2ème étage)

Descriptif : Appartement T5 duplex au 1er étage du bâtiment 2, comprenant au R+1 : entrée, séjour/cuisine, salle d'eau, dégagement, WC, 2 chambres et balcon ; au R+2 : dégagement, salle de bains, WC, mezzanine, 2 chambres et terrasse.

Accès par l'escalier C depuis la porte gauche sur le palier.

Il correspond aux 1817/10000° de la quote-part de l'immeuble Bâtiment 2

Il correspond aux 523/10000° de la quote-part de l'ensemble immobilier

Il correspond aux 0/10000° de la quote-part des charges d'ascenseur de l'immeuble Bâtiment 2

Il correspond aux 5547/10000° de la quote-part des charges d'escalier C de l'immeuble Bâtiment 2

Description du lot dénommé : Lot 16 (situé au 1er étage, 2ème étage)

Descriptif : Appartement T5 duplex au 1er étage du bâtiment 2, comprenant au R+1 : entrée, séjour/cuisine, salle de bains/WC, chambre et balcon ; au R+2 : dégagement, salle de bains, WC, mezzanine et 3 chambres.

Accès par l'escalier C depuis la porte droite sur le palier.

Il correspond aux 1432/10000° de la quote-part de l'immeuble Bâtiment 2

Il correspond aux 412/10000° de la quote-part de l'ensemble immobilier

Il correspond aux 0/10000° de la quote-part des charges d'ascenseur de l'immeuble Bâtiment 2

Il correspond aux 4453/10000° de la quote-part des charges d'escalier C de l'immeuble Bâtiment 2

Description du lot dénommé : Lot 17 (situé au 1er étage)

Descriptif : Appartement T3 au 1er étage du bâtiment 2, comprenant : entrée, séjour/cuisine, dégagement, salle de bains, WC, 2 chambres et balcon.

Accès par l'escalier B depuis la porte gauche sur le palier.

Il correspond aux 961/10000° de la quote-part de l'immeuble Bâtiment 2

Il correspond aux 277/10000° de la quote-part de l'ensemble immobilier

Il correspond aux 2384/10000° de la quote-part des charges d'ascenseur de l'immeuble Bâtiment 2

Il correspond aux 2441/10000° de la quote-part des charges d'escalier B de l'immeuble Bâtiment 2

Description du lot dénommé : Lot 18 (situé au 1er étage)

Descriptif : Appartement T3 au 1er étage du bâtiment 2, comprenant : entrée, séjour/cuisine, dégagement, salle de bains, WC, 2 chambres et balcon.

Accès par l'escalier B depuis la porte droite sur le palier.

Il correspond aux 914/10000° de la quote-part de l'immeuble Bâtiment 2

Il correspond aux 263/10000° de la quote-part de l'ensemble immobilier

Il correspond aux 2267/10000° de la quote-part des charges d'ascenseur de l'immeuble Bâtiment 2

Il correspond aux 2321/10000° de la quote-part des charges d'escalier B de l'immeuble Bâtiment 2

Description du lot dénommé : Lot 19 (situé au 2ème étage)

Descriptif : Appartement T3 au 2ème étage du bâtiment 2, comprenant : entrée, séjour/cuisine, dégagement, salle de bains, WC, 2 chambres et balcon.

Accès par l'escalier B depuis la porte gauche sur le palier.

Il correspond aux 980/10000° de la quote-part de l'immeuble Bâtiment 2

Il correspond aux 282/10000° de la quote-part de l'ensemble immobilier

Il correspond aux 2742/10000° de la quote-part des charges d'ascenseur de l'immeuble Bâtiment 2

Il correspond aux 2685/10000° de la quote-part des charges d'escalier B de l'immeuble Bâtiment 2

**Description du lot dénommé : Lot 20** (situé au 2ème étage)

Descriptif : Appartement T3 au 2ème étage du bâtiment 2, comprenant : entrée, séjour/cuisine, dégagement, salle de bains, WC, 2 chambres et balcon.

Accès par l'escalier B depuis la porte droite sur le palier.

Il correspond aux 932/10000° de la quote-part de l'immeuble Bâtiment 2

Il correspond aux 268/10000° de la quote-part de l'ensemble immobilier

Il correspond aux 2607/10000° de la quote-part des charges d'ascenseur de l'immeuble Bâtiment 2

Il correspond aux 2553/10000° de la quote-part des charges d'escalier B de l'immeuble Bâtiment 2

Description du lot dénommé : Lot 21 (situé au Rez-de-jardin)

Descriptif : Garage PMR au rez-de-jardin du bâtiment 2, portant le numéro 1 du plan des garages.

Accès direct par l'extérieur depuis le boulevard des Allées.

Il correspond aux 130/10000° de la quote-part de l'immeuble Bâtiment 2

Il correspond aux 37/10000° de la quote-part de l'ensemble immobilier

Il correspond aux 0/10000° de la quote-part des charges d'ascenseur de l'immeuble Bâtiment 2

Il correspond aux 0/10000° de la quote-part des charges d'escalier de l'immeuble Bâtiment 2

Description du lot dénommé : Lot 22 (situé au Rez-de-jardin)

Descriptif : Garage au rez-de-jardin du bâtiment 2, portant le numéro 2 du plan des garages.

Accès direct par l'extérieur depuis le boulevard des Allées.

Il correspond aux 112/10000° de la quote-part de l'immeuble Bâtiment 2

Il correspond aux 32/10000° de la quote-part de l'ensemble immobilier

Il correspond aux 0/10000° de la quote-part des charges d'ascenseur de l'immeuble Bâtiment 2

Il correspond aux 0/10000° de la quote-part des charges d'escalier de l'immeuble Bâtiment 2

Description du lot dénommé : Lot 23 (situé au Rez-de-jardin)

Descriptif : Garage au rez-de-jardin du bâtiment 2, portant le numéro 3 du plan des garages.

Accès direct par l'extérieur depuis le boulevard des Allées.

Il correspond aux 112/10000° de la quote-part de l'immeuble Bâtiment 2

Il correspond aux 32/10000° de la quote-part de l'ensemble immobilier

Il correspond aux 0/10000° de la quote-part des charges d'ascenseur de l'immeuble Bâtiment 2

Il correspond aux 0/10000° de la quote-part des charges d'escalier de l'immeuble Bâtiment 2

Description du lot dénommé : Lot 24 (situé au Rez-de-jardin)

Descriptif : Garage PMR au rez-de-jardin du bâtiment 2, portant le numéro 4 du plan des garages.

Accès direct par l'extérieur depuis le boulevard des Allées.

Il correspond aux 148/10000° de la quote-part de l'immeuble Bâtiment 2

Il correspond aux 43/10000° de la quote-part de l'ensemble immobilier

Il correspond aux 0/10000° de la quote-part des charges d'ascenseur de l'immeuble Bâtiment 2

Il correspond aux 0/10000° de la quote-part des charges d'escalier de l'immeuble Bâtiment 2

Description du lot dénommé : Lot 25 (situé au Rez-de-jardin)

Descriptif : Garage au rez-de-jardin du bâtiment 2, portant le numéro 5 du plan des garages.

Accès direct par l'extérieur depuis le boulevard des Allées.

Il correspond aux 105/10000° de la quote-part de l'immeuble Bâtiment 2

Il correspond aux 30/10000° de la quote-part de l'ensemble immobilier

Il correspond aux 0/10000° de la quote-part des charges d'ascenseur de l'immeuble Bâtiment 2

Il correspond aux 0/10000° de la quote-part des charges d'escalier de l'immeuble Bâtiment 2

Description du lot dénommé : Lot 26 (situé au Rez-de-jardin)

Descriptif : Garage au rez-de-jardin du bâtiment 2, portant le numéro 6 du plan des garages.

Accès direct par l'extérieur depuis le boulevard des Allées.

Il correspond aux 105/10000° de la quote-part de l'immeuble Bâtiment 2

Il correspond aux 30/10000° de la quote-part de l'ensemble immobilier

Il correspond aux 0/10000° de la quote-part des charges d'ascenseur de l'immeuble Bâtiment 2

Il correspond aux 0/10000° de la quote-part des charges d'escalier de l'immeuble Bâtiment 2

Description du lot dénommé : Lot 27 (situé au Rez-de-jardin)

Descriptif : Garage au rez-de-jardin du bâtiment 2, portant le numéro 7 du plan des garages.

Accès direct par l'extérieur depuis le boulevard des Allées.

Il correspond aux 110/10000° de la quote-part de l'immeuble Bâtiment 2

Il correspond aux 32/10000° de la quote-part de l'ensemble immobilier

Il correspond aux 0/10000° de la quote-part des charges d'ascenseur de l'immeuble Bâtiment 2

Il correspond aux 0/10000° de la quote-part des charges d'escalier de l'immeuble Bâtiment 2



Emplacements de stationnement extérieur

Description du lot dénommé : Lot 28 (situé au Rez-de-jardin)

Descriptif : Emplacement de parking au rez-de-jardin du bâtiment 2, portant le numéro 1 du plan des parkings.

Accès direct par l'extérieur depuis le boulevard des Allées.

Il correspond aux 5/10000° de la quote-part de l'ensemble immobilier

Il correspond aux 504/10000° de la quote-part des charges spéciales « Emplacements de stationnement extérieur »

Description du lot dénommé : Lot 29 (situé au Rez-de-jardin)

Descriptif : Emplacement de parking au rez-de-jardin du bâtiment 2, portant le numéro 2 du plan des parkings.

Accès direct par l'extérieur depuis le boulevard des Allées.

Il correspond aux 5/10000° de la quote-part de l'ensemble immobilier

Il correspond aux 504/10000° de la quote-part des charges spéciales « Emplacements de stationnement extérieur »

Description du lot dénommé : Lot 30 (situé au Rez-de-jardin)

Descriptif : Emplacement de parking au rez-de-jardin du bâtiment 2, portant le numéro 4 du plan des parkings.

Accès direct par l'extérieur depuis le boulevard des Allées.

Il correspond aux 5/10000° de la quote-part de l'ensemble immobilier

Il correspond aux 556/10000° de la quote-part des charges spéciales « Emplacements de stationnement extérieur »

Description du lot dénommé : Lot 31 (situé au Rez-de-jardin)

Descriptif : Emplacement de parking au rez-de-jardin du bâtiment 2, portant le numéro 5 du plan des parkings.

Accès direct par l'extérieur depuis le boulevard des Allées.

Il correspond aux 5/10000° de la quote-part de l'ensemble immobilier

Il correspond aux 556/10000° de la quote-part des charges spéciales « Emplacements de stationnement extérieur »

Description du lot dénommé : Lot 32 (situé au Rez-de-jardin)

Descriptif : Emplacement de parking au rez-de-jardin du bâtiment 2, portant le numéro 6 du plan des parkings.

Accès direct par l'extérieur depuis le boulevard des Allées.

Il correspond aux 5/10000° de la quote-part de l'ensemble immobilier

Il correspond aux 570/10000° de la quote-part des charges spéciales « Emplacements de stationnement extérieur »

Description du lot dénommé : Lot 33 (situé au Rez-de-jardin)

Descriptif : Emplacement de parking au rez-de-jardin du bâtiment 2, portant le numéro 7 du plan des parkings.

Accès direct par l'extérieur depuis le boulevard des Allées.

Il correspond aux 5/10000° de la quote-part de l'ensemble immobilier

Il correspond aux 570/10000° de la quote-part des charges spéciales « Emplacements de stationnement extérieur »

Description du lot dénommé : Lot 34 (situé au Rez-de-jardin)

Descriptif : Emplacement de parking au rez-de-jardin du bâtiment 2, portant le numéro 10 du plan des parkings.

Accès direct par l'extérieur depuis le boulevard des Allées.

Il correspond aux 5/10000° de la quote-part de l'ensemble immobilier

Il correspond aux 504/10000° de la quote-part des charges spéciales « Emplacements de stationnement extérieur »

Description du lot dénommé : Lot 35 (situé au Rez-de-jardin)

Descriptif : Emplacement de parking au rez-de-jardin du bâtiment 2, portant le numéro 11 du plan des parkings.

Accès direct par l'extérieur depuis le boulevard des Allées.

Il correspond aux 5/10000° de la quote-part de l'ensemble immobilier

Il correspond aux 504/10000° de la quote-part des charges spéciales « Emplacements de stationnement extérieur »

Description du lot dénommé : Lot 36 (situé au Rez-de-jardin)

Descriptif : Emplacement de parking au rez-de-jardin du bâtiment 2, portant le numéro 12 du plan des parkings.

Accès direct par l'extérieur depuis le boulevard des Allées.

Il correspond aux 5/10000° de la quote-part de l'ensemble immobilier

Il correspond aux 504/10000° de la quote-part des charges spéciales « Emplacements de stationnement extérieur »

Description du lot dénommé : Lot 37 (situé au Rez-de-jardin)

Descriptif : Emplacement de parking au rez-de-jardin du bâtiment 2, portant le numéro 13 du plan des parkings.

Accès direct par l'extérieur depuis le boulevard des Allées.

Il correspond aux 5/10000° de la quote-part de l'ensemble immobilier

Il correspond aux 504/10000° de la quote-part des charges spéciales « Emplacements de stationnement extérieur »

**Description du lot dénommé : Lot 38** (situé au Rez-de-jardin)

Descriptif : Emplacement de parking PMR au rez-de-jardin du bâtiment 2, portant le numéro 14 du plan des parkings.

Accès direct par l'extérieur depuis le boulevard des Allées.

Il correspond aux 7/10000° de la quote-part de l'ensemble immobilier

Il correspond aux 692/10000° de la quote-part des charges spéciales « Emplacements de stationnement extérieur »

Description du lot dénommé : Lot 39 (situé au Rez-de-jardin)

Descriptif : Emplacement de parking au rez-de-jardin du bâtiment 2, portant le numéro 15 du plan des parkings.

Accès direct par l'extérieur depuis le boulevard des Allées.

Il correspond aux 5/10000° de la quote-part de l'ensemble immobilier

Il correspond aux 504/10000° de la quote-part des charges spéciales « Emplacements de stationnement extérieur »

Description du lot dénommé : Lot 40 (situé au Rez-de-jardin)

Descriptif : Emplacement de parking au rez-de-jardin du bâtiment 2, portant le numéro 16 du plan des parkings.

Accès direct par l'extérieur depuis le boulevard des Allées.

Il correspond aux 5/10000° de la quote-part de l'ensemble immobilier

Il correspond aux 504/10000° de la quote-part des charges spéciales « Emplacements de stationnement extérieur »

Description du lot dénommé : Lot 41 (situé au Rez-de-jardin)

Descriptif : Emplacement de parking au rez-de-jardin du bâtiment 2, portant le numéro 17 du plan des parkings.

Accès direct par l'extérieur depuis le boulevard des Allées.

Il correspond aux 5/10000° de la quote-part de l'ensemble immobilier

Il correspond aux 504/10000° de la quote-part des charges spéciales « Emplacements de stationnement extérieur »

Description du lot dénommé : Lot 42 (situé au Rez-de-jardin)

Descriptif : Emplacement de parking au rez-de-jardin du bâtiment 2, portant le numéro 18 du plan des parkings.

Accès direct par l'extérieur depuis le boulevard des Allées.

Il correspond aux 5/10000° de la quote-part de l'ensemble immobilier

Il correspond aux 504/10000° de la quote-part des charges spéciales « Emplacements de stationnement extérieur »

Description du lot dénommé : Lot 43 (situé au Rez-de-jardin)

Descriptif : Emplacement de parking au rez-de-jardin du bâtiment 2, portant le numéro 19 du plan des parkings.

Accès direct par l'extérieur depuis le boulevard des Allées.

Il correspond aux 5/10000° de la quote-part de l'ensemble immobilier

Il correspond aux 504/10000° de la quote-part des charges spéciales « Emplacements de stationnement extérieur »

Description du lot dénommé : Lot 44 (situé au Rez-de-jardin)

Descriptif : Emplacement de parking au rez-de-jardin du bâtiment 2, portant le numéro 20 du plan des parkings.

Accès direct par l'extérieur depuis le boulevard des Allées.

Il correspond aux 5/10000° de la quote-part de l'ensemble immobilier

Il correspond aux 504/10000° de la quote-part des charges spéciales « Emplacements de stationnement extérieur »

Description du lot dénommé : Lot 45 (situé au Rez-de-jardin)

Descriptif : Emplacement de parking au rez-de-jardin du bâtiment 2, portant le numéro 21 du plan des parkings.

Accès direct par l'extérieur depuis le boulevard des Allées.

Il correspond aux 5/10000° de la quote-part de l'ensemble immobilier

Il correspond aux 504/10000° de la quote-part des charges spéciales « Emplacements de stationnement extérieur »

Description du lot dénommé : Lot 46 (situé au Rez-de-jardin)

Descriptif : Emplacement de parking au rez-de-jardin du bâtiment 2, portant le numéro 22 du plan des parkings.

Accès direct par l'extérieur depuis le boulevard des Allées.

Il correspond aux 5/10000° de la quote-part de l'ensemble immobilier

Il correspond aux 504/10000° de la quote-part des charges spéciales « Emplacements de stationnement extérieur »

G. - Récapitulatif des lots :

L'état descriptif de division est résumé dans un tableau récapitulatif établi conformément à l'article 71 du décret numéro 55-1350 du 14 Octobre 1955, modifié par le décret numéro 59- 90 du 7 Janvier 1959, pris pour l'application du décret numéro 55-22 du 4 Janvier 1955 portant réforme de la publicité foncière.

Ce tableau est ci-après établi en fin des présentes.

Il est ici précisé que les calculs de fixation des quotes-parts de parties communes et de répartition des charges ont été réalisés selon la consistance, la superficie et la situation de chaque lot sans égard à leur utilisation.



Bâtiment 1

N° Lot	Etage	Nature	Surface	Surface pondérée	Quote-part des parties communes sur le bâtiment (1/10000)	Quote-part des parties communes sur l'ensemble immobilier (1/10000)	Quote-part ascenseur (1/10000)	Quote-part escalier A (1/10000)
Lot 1	Rez-de-jardin	Bureau	94.05	200.44	1135	798	0	0
Lot 2	Rez-de-jardin	Bureau	100.00	208.86	1183	832	0	0
Lot 3	Rez-de-chaussée	Local commercial	160.00	346.21	1962	1379	0	0
Lot 4	Rez-de-chaussée	Local commercial	170.50	376.46	2134	1499	0	0
Lot 5	1er étage	Appartement	48.15					
Lot 5	1er étage	Balcon	3.00					
Total Lot 5			51.15	48.32	274	192	617	643
Lot 6	1er étage	Appartement	56.35					
Lot 6	1er étage	Balcon	3.10					
Total Lot 6			59.45	56.39	320	225	720	750
Lot 7	1er étage	Appartement	69.00					
Lot 7	1er étage	Terrasse	14.64					
Total Lot 7			83.64	76.35	433	304	936	975
Lot 8	1er étage	Appartement	87.55					
Lot 8	1er étage	Terrasse	16.90					
Total Lot 8			104.45	96.2	545	383	1180	1228
Lot 9	2ème étage	Appartement	44.60					
Lot 9	2ème étage	Balcon	8.45					
Lot 9	3ème étage	Appartement	48.30					
Total Lot 9			101.35	79.85	453	318	1475	1442
Lot 10	2ème étage	Appartement	44.00					
Lot 10	2ème étage	Balcon	6.95					
Lot 10	3ème étage	Appartement	43.30					
Total Lot 10			94.25	73.14	415	291	1377	1347
Lot 11	2ème étage	Appartement	49.00					
Lot 11	2ème étage	Balcon	22.65					
Lot 11	3ème étage	Appartement	53.35					
Total Lot 11			125	91.49	519	364	1703	1666
Lot 12	2ème étage	Appartement	57.95					
Lot 12	2ème étage	Balcon	26.10					
Lot 12	3ème étage	Appartement	62.02					
Total Lot 12			146.07	110.57	627	440	1992	1949
TOTAL			1289.91	1764.29	10000	7025	10000	10000



Bâtiment 2

N° Lot	Etage	Nature	Surface	Surface pondérée	Quote-part des parties communes sur le bâtiment (1/10000)	Quote-part des parties communes sur l'ensemble immobilier (1/10000)	Quote-part ascenseur (1/10000)	Quote-part escalier B (1/10000)	Quote-part escalier C (1/10000)
Lot 13	Rez-de-jardin	Appartement	68.90						
Lot 13	Rez-de-jardin	Terrasse	8.00						
Lot 13	Rez-de-jardin	Jardin privé	31.55						
Total Lot 13			108.45	76.97	1065	307	0	0	
Lot 14	Rez-de-jardin	Appartement	64.70						
Lot 14	Rez-de-jardin	Terrasse	8.00						
Lot 14	Rez-de-jardin	Jardin privé	57.65						
Total Lot 14			130.35	77.84	1077	310	0	0	
Lot 15	1er étage	Appartement	67.65						
Lot 15	1er étage	Balcon	30.25						
Lot 15	2ème étage	Appartement	45.10						
Lot 15	2ème étage	Terrasse	10.45						
Total Lot 15			153.45	131.22	1817	523	0	0	5547
Lot 16	1er étage	Appartement	51.10						
Lot 16	1er étage	Balcon	4.85						
Lot 16	2ème étage	Appartement	49.55						
Total Lot 16			105.5	103.52	1432	412	0	0	4453
Lot 17	1er étage	Appartement	67.35						
Lot 17	1er étage	Balcon	5.35						
Total Lot 17			72.7	69.46	961	277	2384	2441	
Lot 18	1er étage	Appartement	63.35						
Lot 18	1er étage	Balcon	6.80						
Total Lot 18			70.15	66.04	914	263	2267	2321	
Lot 19	2ème étage	Appartement	67.35						
Lot 19	2ème étage	Balcon	5.35						
Total Lot 19			72.7	70.82	980	282	2742	2685	
Lot 20	2ème étage	Appartement	63.35						
Lot 20	2ème étage	Balcon	6.80						
Total Lot 20			70.15	67.34	932	268	2607	2553	
Lot 21	Rez-de-jardin	Garage	15.66	9.40	130	37	0	0	0
Lot 22	Rez-de-jardin	Garage	13.50	8.10	112	32	0	0	0
Lot 23	Rez-de-jardin	Garage	13.50	8.10	112	32	0	0	0
Lot 24	Rez-de-jardin	Garage	17.80	10.68	148	43	0	0	0
Lot 25	Rez-de-jardin	Garage	12.70	7.62	105	30	0	0	0
Lot 26	Rez-de-jardin	Garage	12.70	7.62	105	30	0	0	0
Lot 27	Rez-de-jardin	Garage	13.30	7.98	110	32	0	0	0
TOTAL			882.61	722.71	10000	2878	10000	10000	10000



Emplacements de stationnement extérieur

N° Lot	Etage	Nature	Surface	Surface pondérée	Quote-part des parties communes sur l'ensemble immobilier (1/10000)	Quote-part charges spéciales « Emplacements de stationnement extérieur » (1/10000)
Lot 28	Rez-de-jardin	Parking ouvert	12.00	1.20	5	504
Lot 29	Rez-de-jardin	Parking ouvert	12.00	1.20	5	504
Lot 30	Rez-de-jardin	Parking ouvert	13.25	1.33	5	556
Lot 31	Rez-de-jardin	Parking ouvert	13.25	1.33	5	556
Lot 32	Rez-de-jardin	Parking ouvert	13.60	1.36	5	570
Lot 33	Rez-de-jardin	Parking ouvert	13.60	1.36	5	570
Lot 34	Rez-de-jardin	Parking ouvert	12.00	1.20	5	504
Lot 35	Rez-de-jardin	Parking ouvert	12.00	1.20	5	504
Lot 36	Rez-de-jardin	Parking ouvert	12.00	1.20	5	504
Lot 37	Rez-de-jardin	Parking ouvert	12.00	1.20	5	504
Lot 38	Rez-de-jardin	Parking ouvert	16.50	1.65	7	692
Lot 39	Rez-de-jardin	Parking ouvert	12.00	1.20	5	504
Lot 40	Rez-de-jardin	Parking ouvert	12.00	1.20	5	504
Lot 41	Rez-de-jardin	Parking ouvert	12.00	1.20	5	504
Lot 42	Rez-de-jardin	Parking ouvert	12.00	1.20	5	504
Lot 43	Rez-de-jardin	Parking ouvert	12.00	1.20	5	504
Lot 44	Rez-de-jardin	Parking ouvert	12.00	1.20	5	504
Lot 45	Rez-de-jardin	Parking ouvert	12.00	1.20	5	504
Lot 46	Rez-de-jardin	Parking ouvert	12.00	1.20	5	504
TOTAL			238.20	23.82	97	10000



H. - Commentaires :

Commentaires :

Cet état descriptif a été réalisé sur la base du projet de rénovation du bâtiment 1 et de la construction du bâtiment 2.

Les superficies privatives et les plans utilisés dans le présent rapport ont été communiqués par l'architecte du projet (version février 2023).

La responsabilité de notre cabinet ne saurait être engagée en cas d'erreurs, d'inexactitudes ou de modifications non communiquées des données prises en compte dans ce rapport.

Chauffage et production d'eau chaude individuels.

Absence d'énergies renouvelables.

Fait à **Chonas l'Amballan**, le **03/03/2023**

Par : **Frédéric PERRENOT**


FPE EXPERTISE

189 chemin des Grandes Bruyères
38121 CHONAS L'AMBALLAN
Tél : 04 74 58 70 05




I. - Plans de repérage des lots

Plans de masse résidence

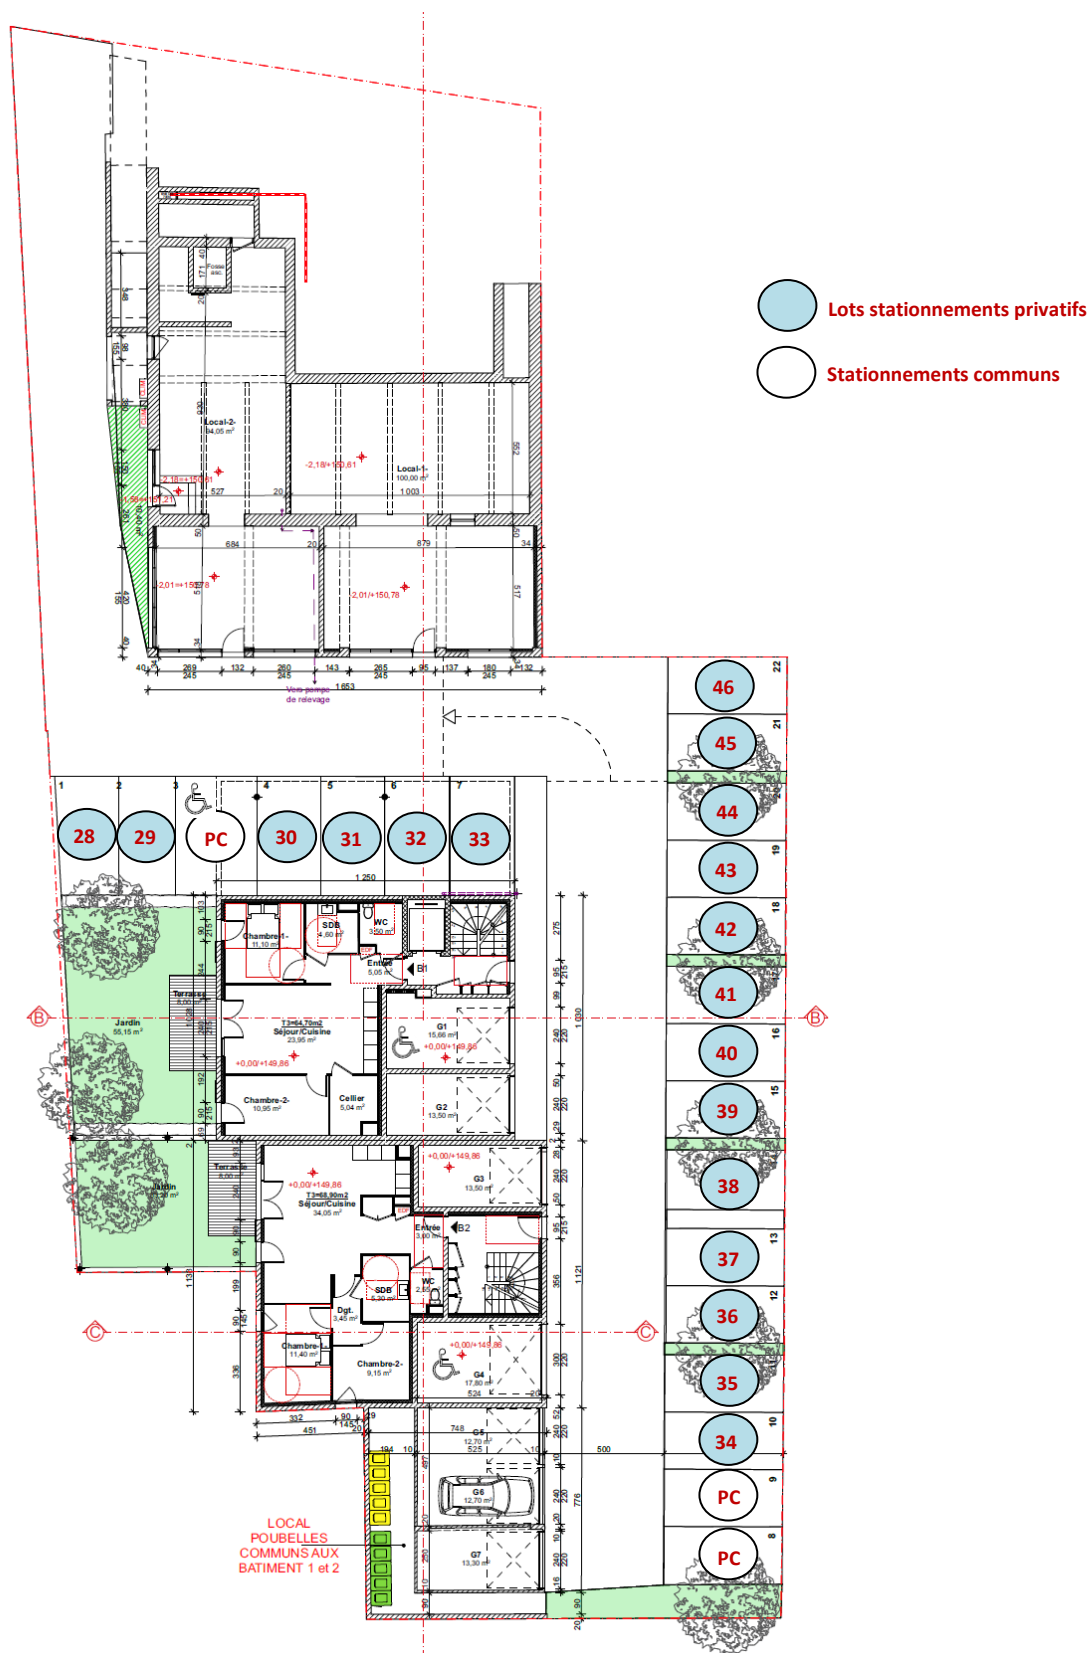




Rez-de-jardin - Bâtiment 1

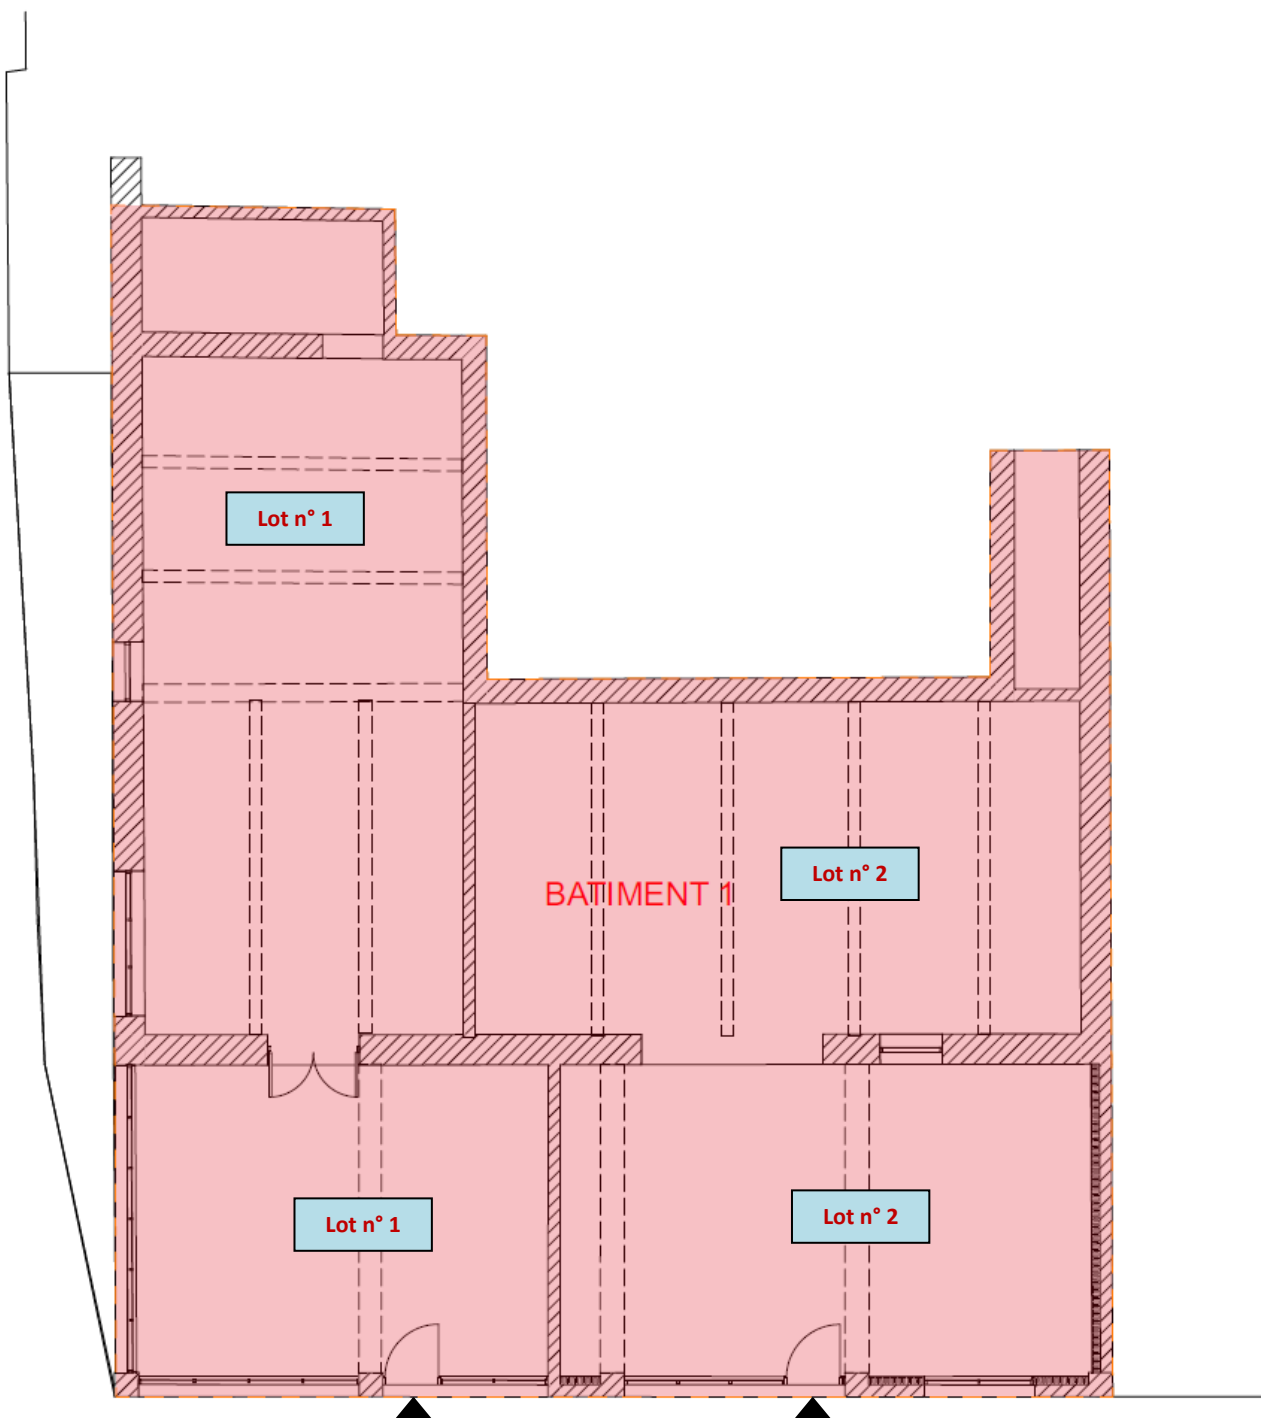




Rez-de-chaussée - Bâtiment 1

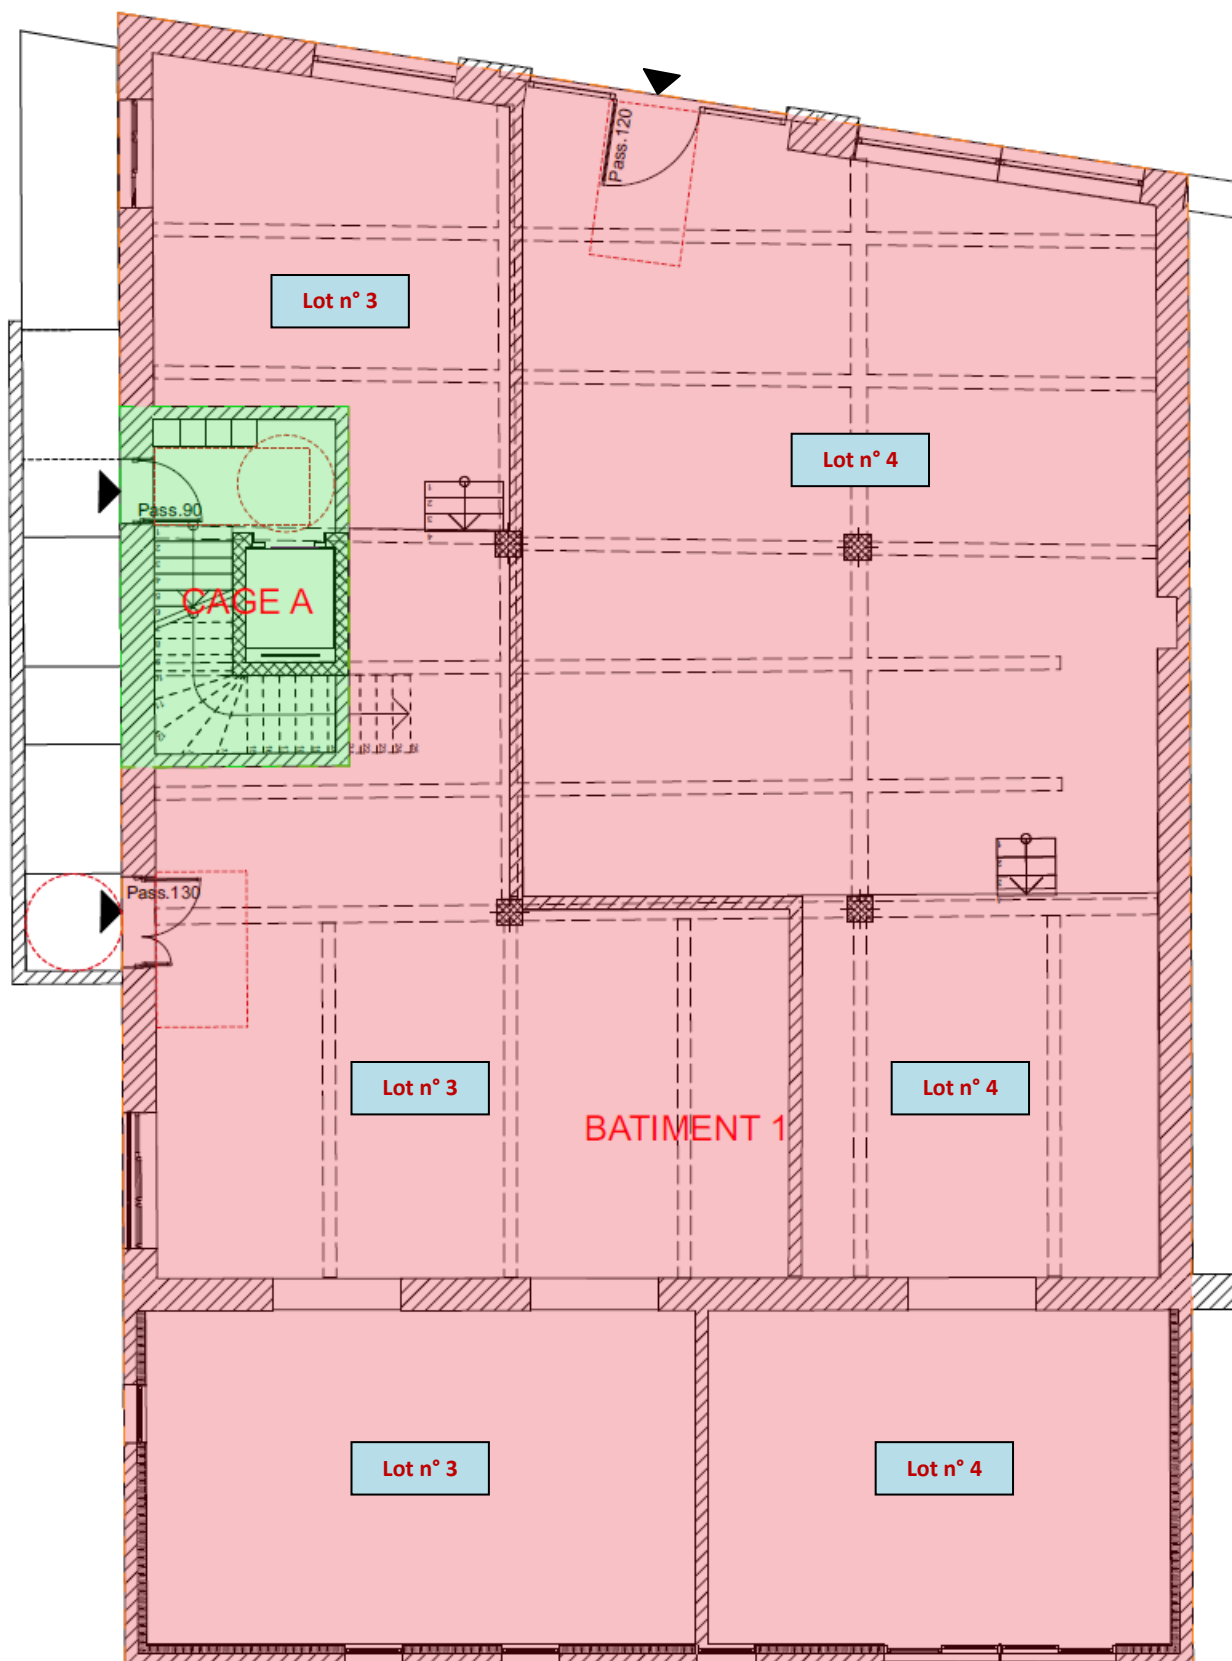




1^{er} étage - Bâtiment 1

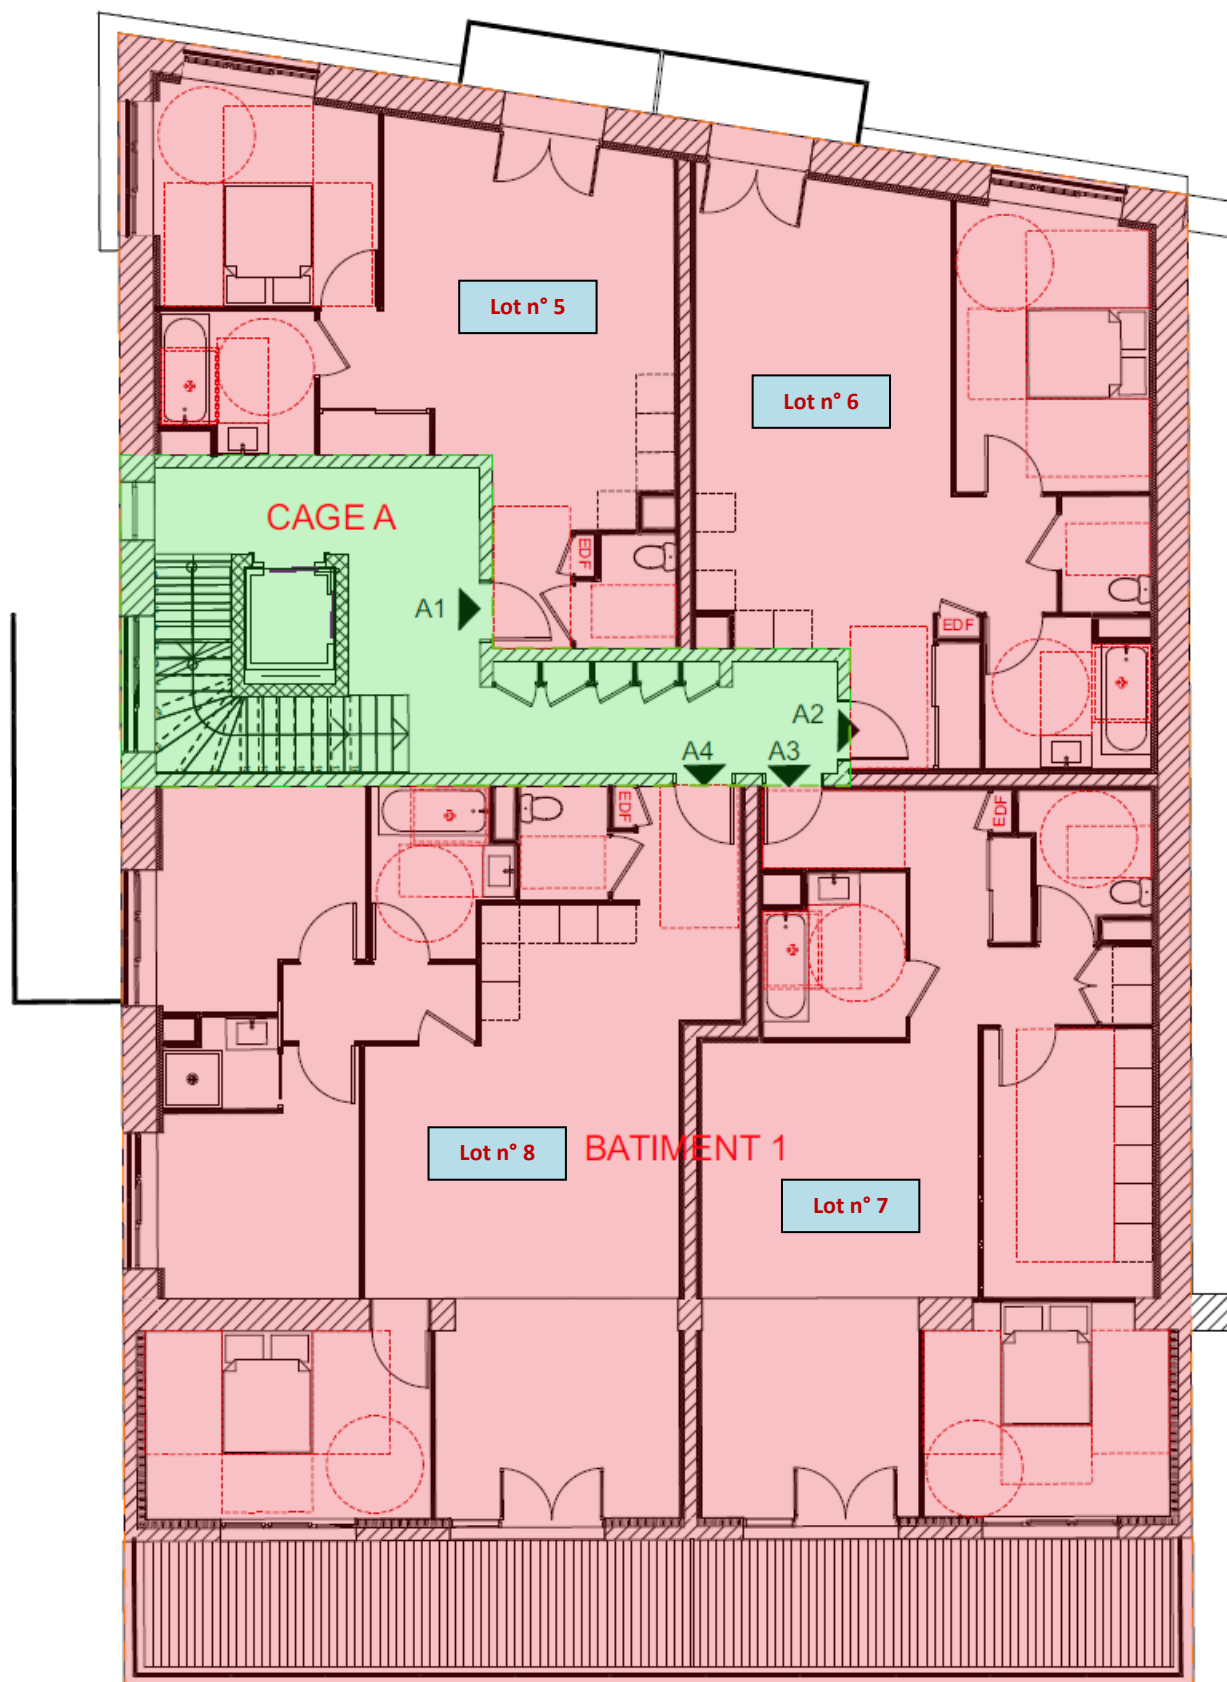




2^{ème} étage - Bâtiment 1

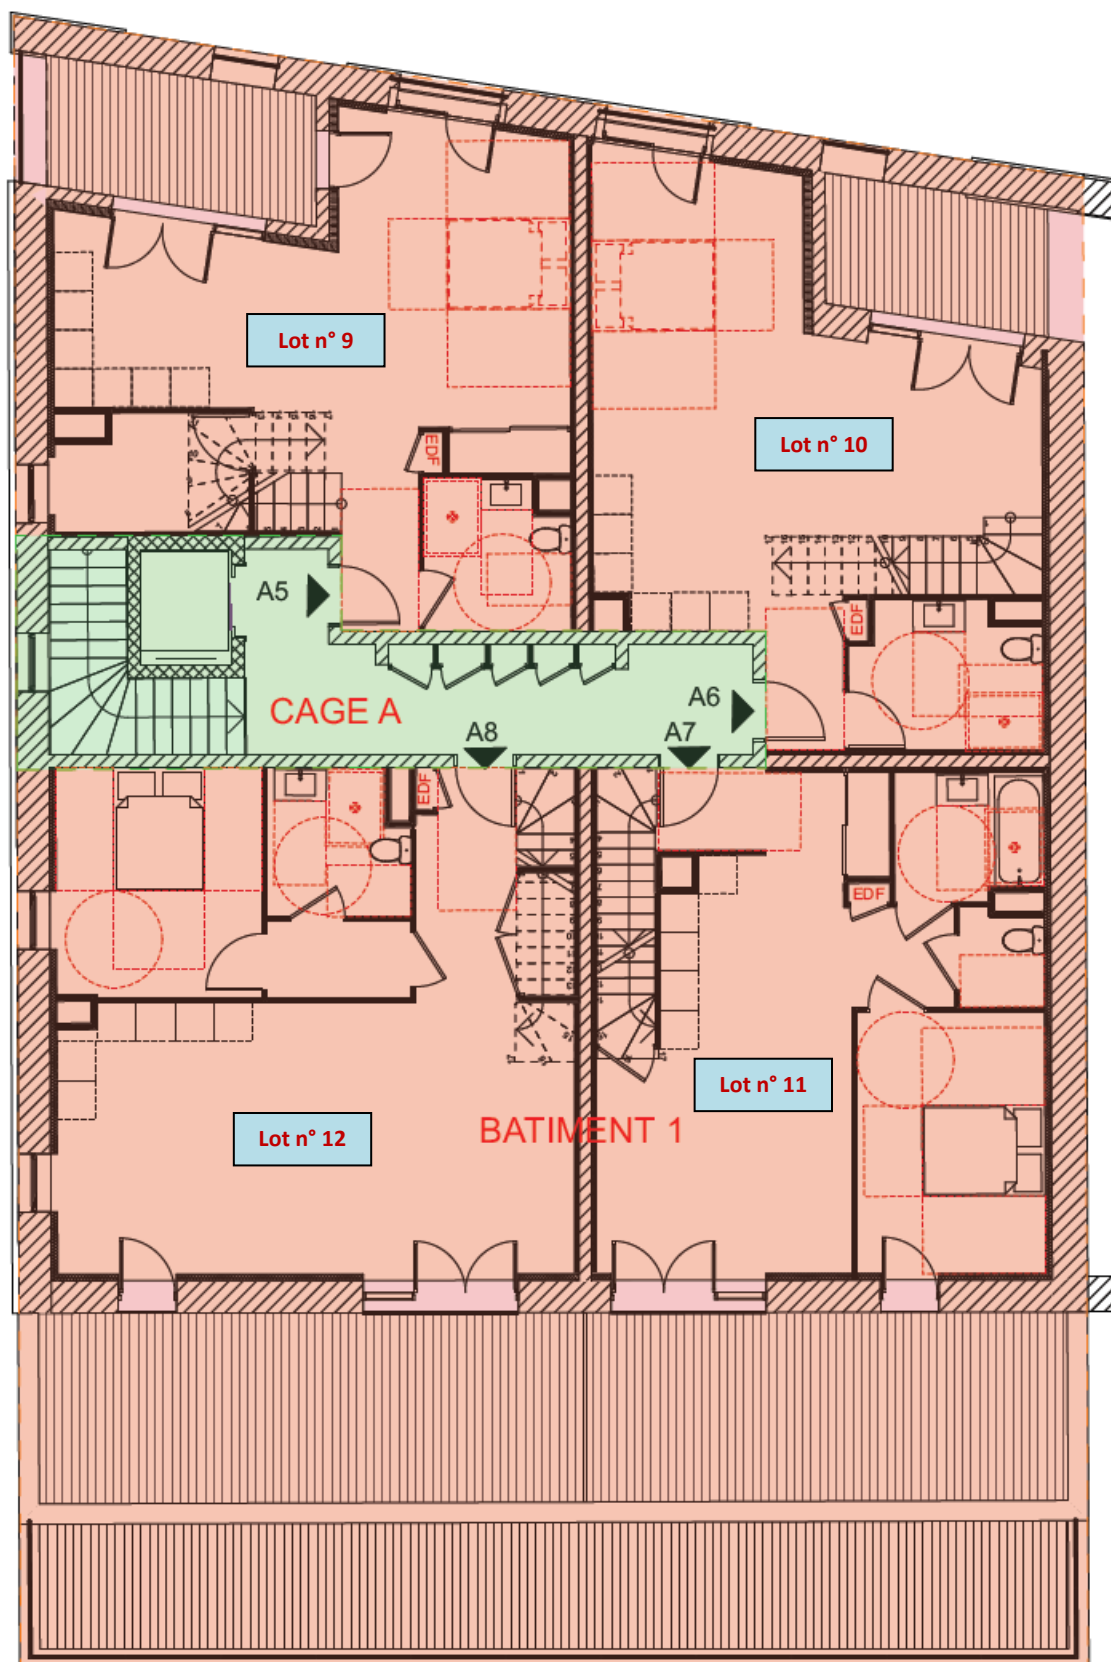




3^{ème} étage - Bâtiment 1

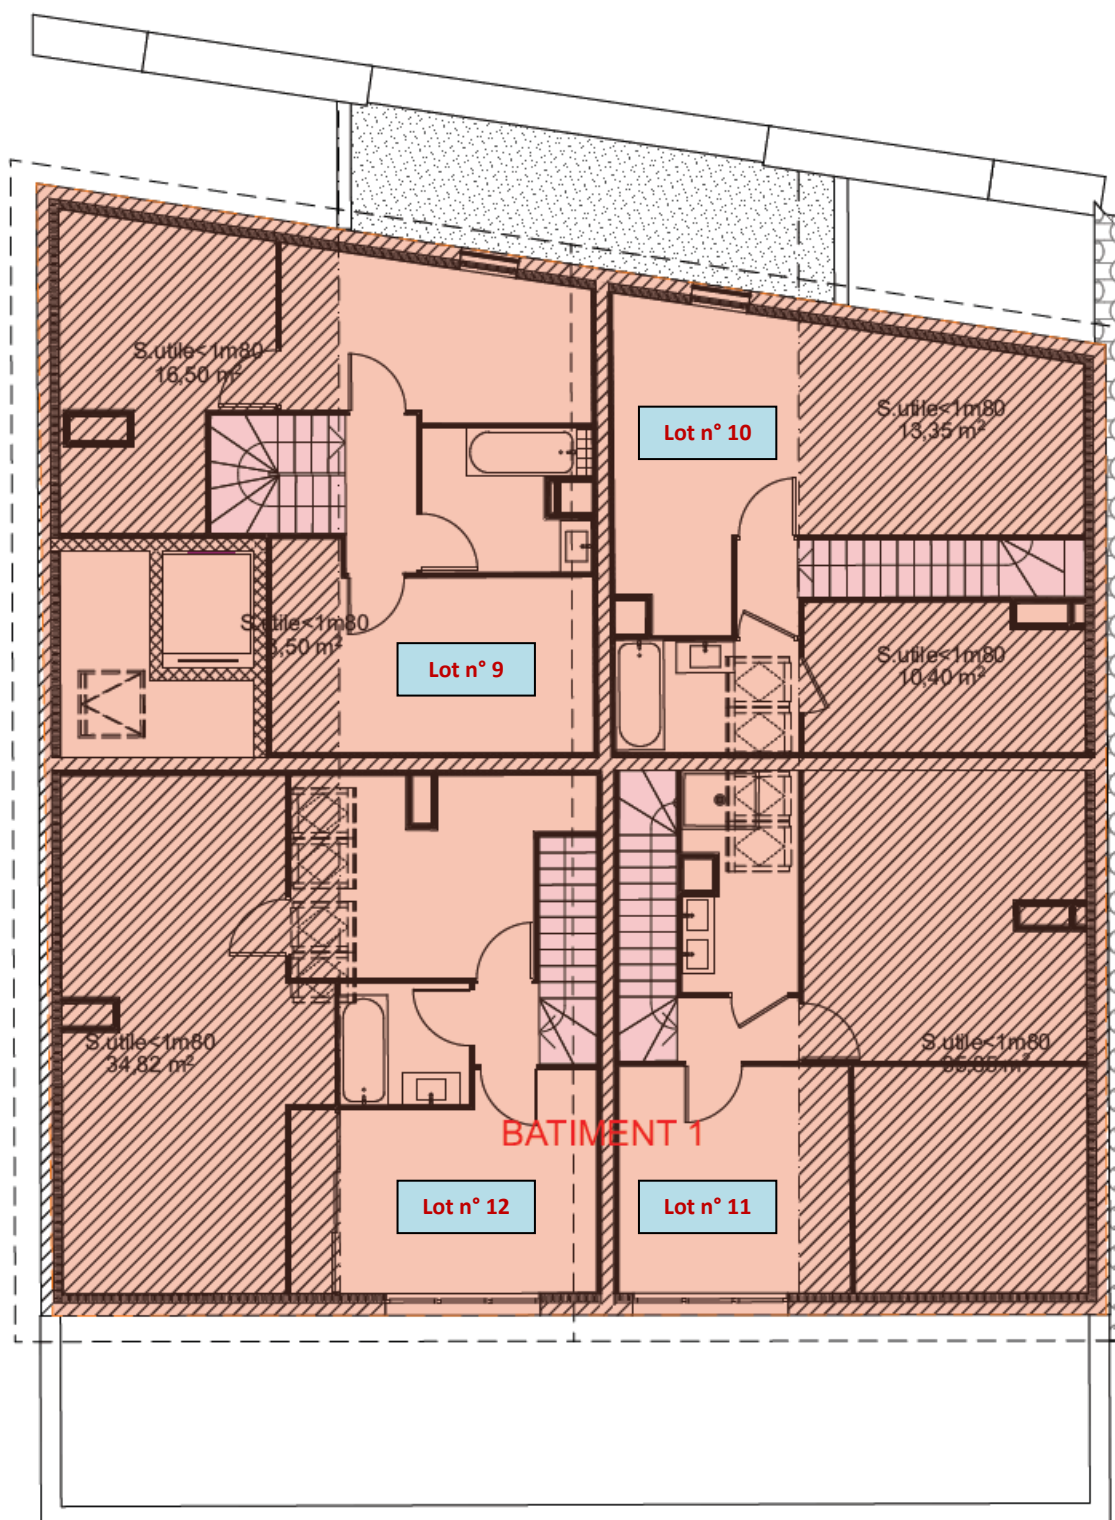




Rez-de-jardin - Bâtiment 2

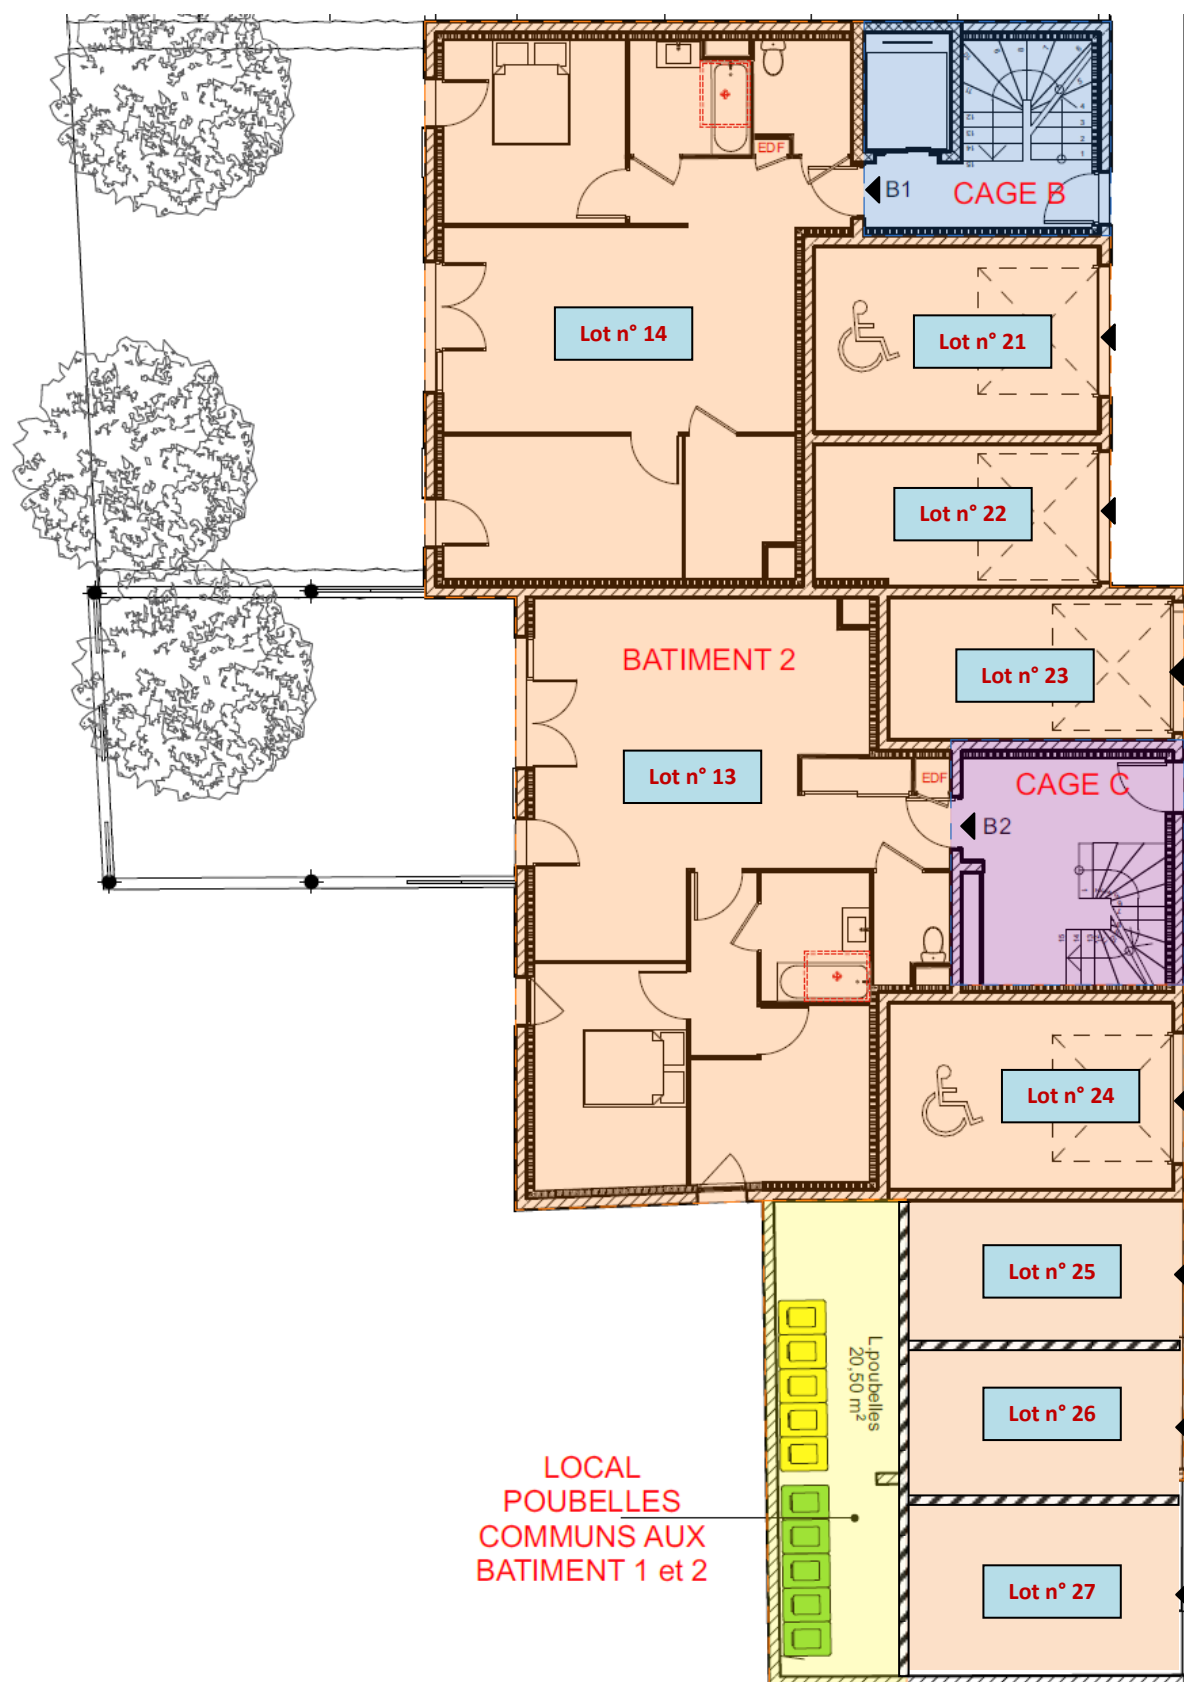


1^{er} étage - Bâtiment 2

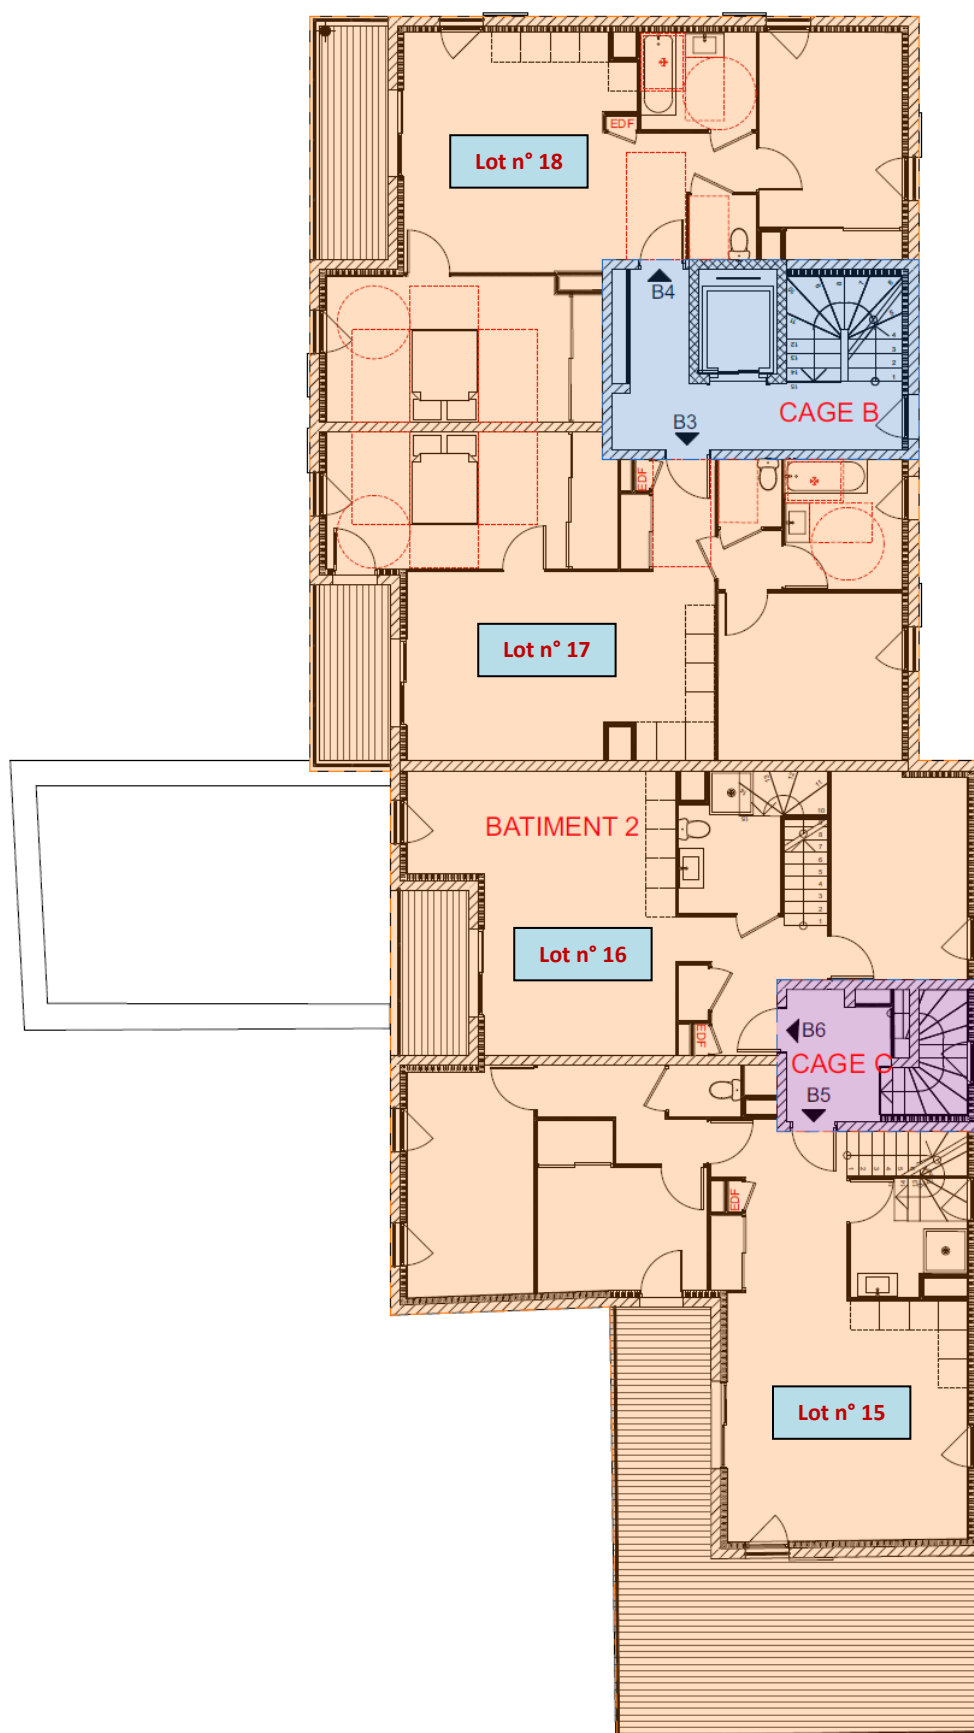




2^{ème} étage - Bâtiment 2

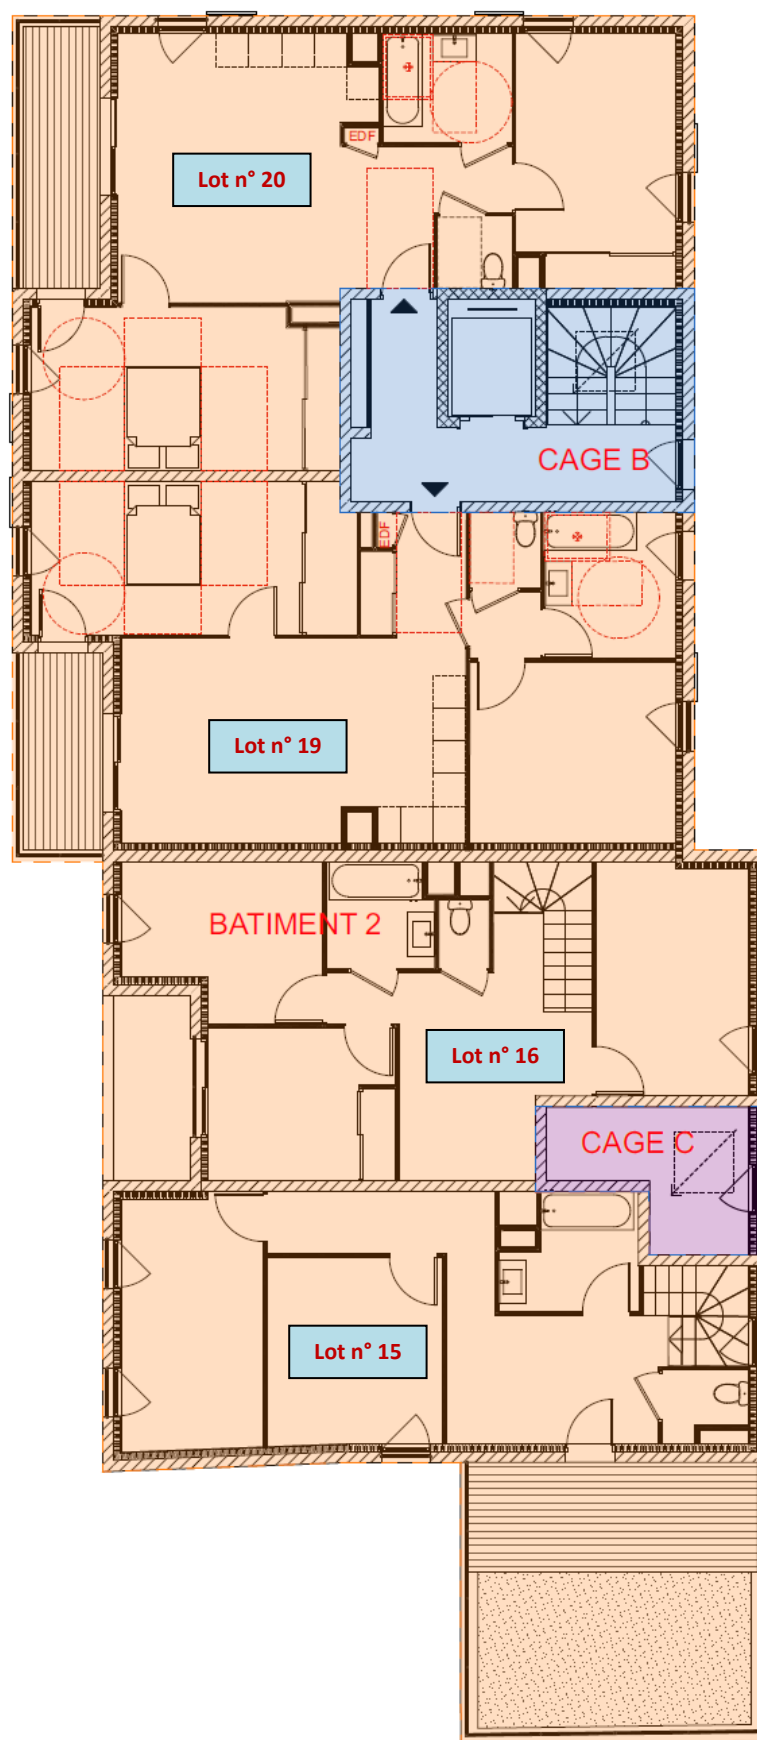





J. - Plans détaillés des lots


Rez-de-jardin - Bâtiment 1

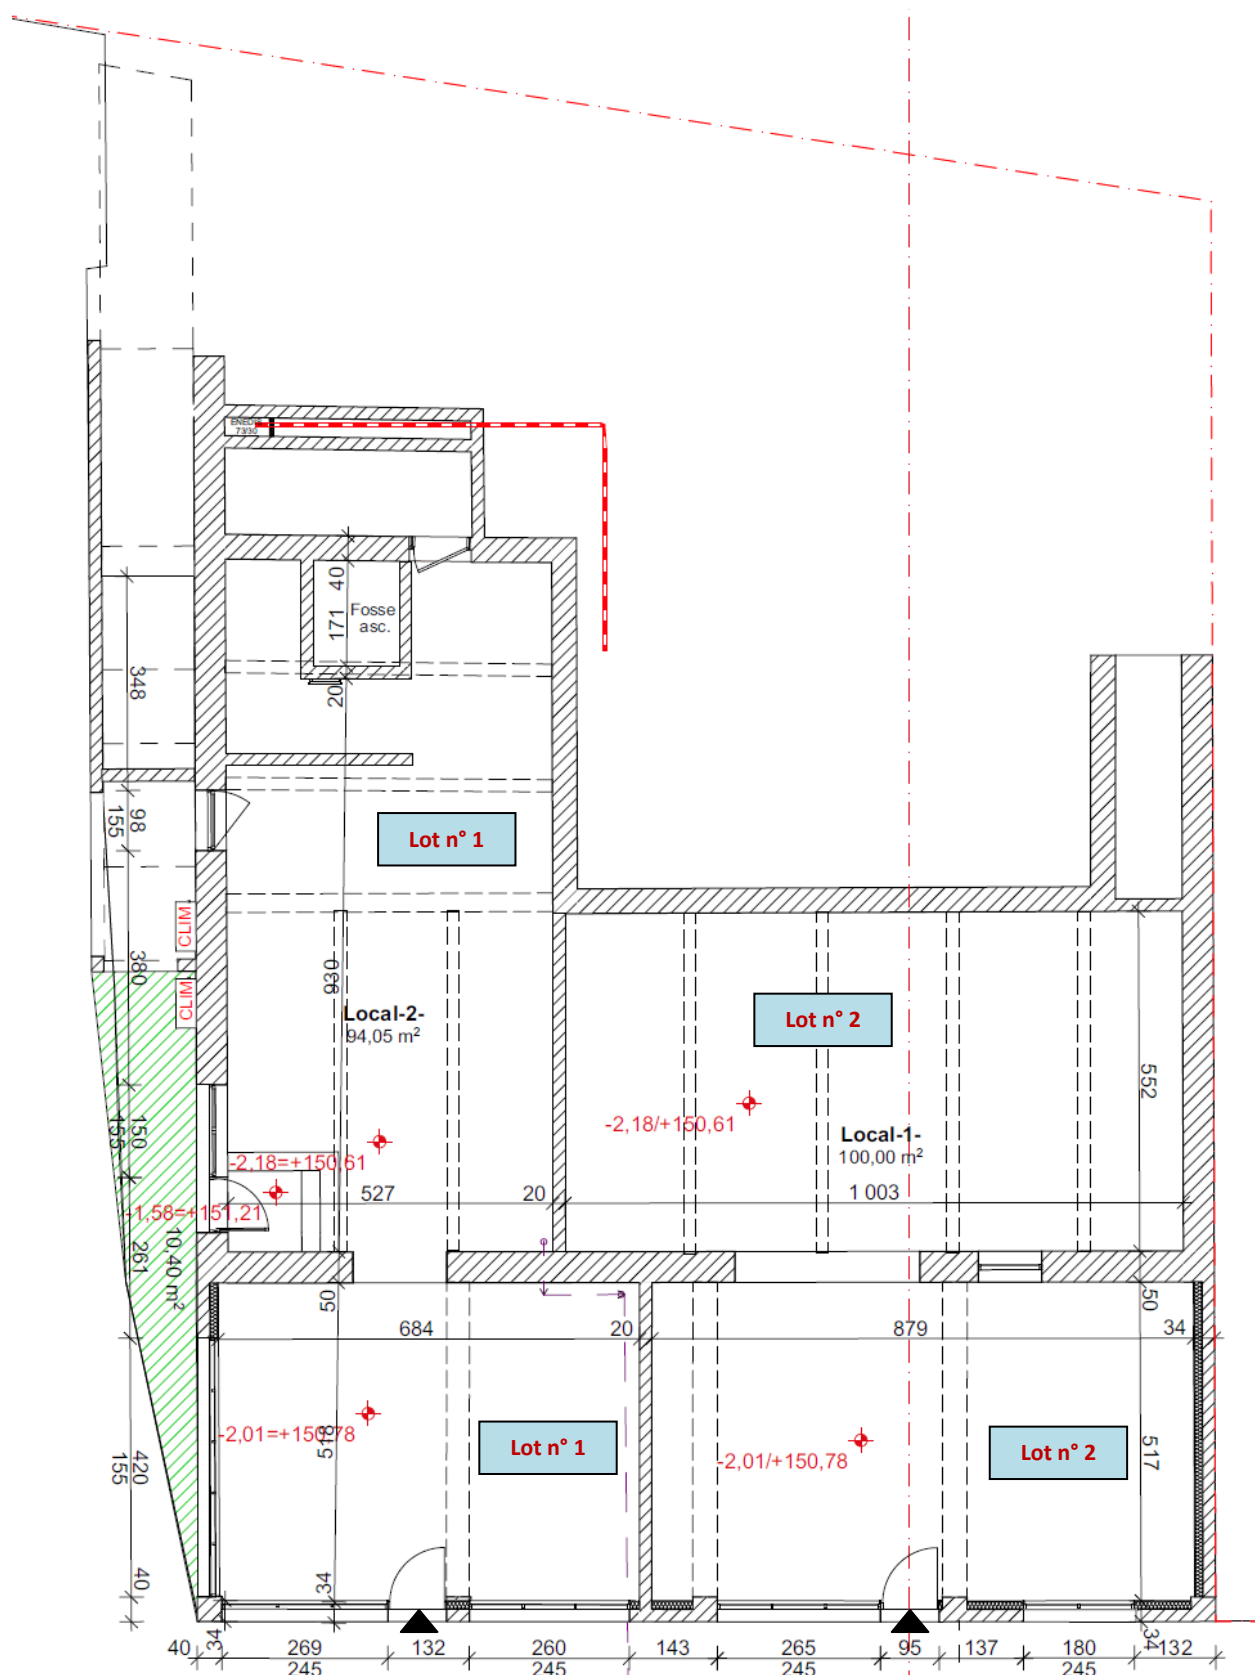


Rez-de-chaussée - Bâtiment 1

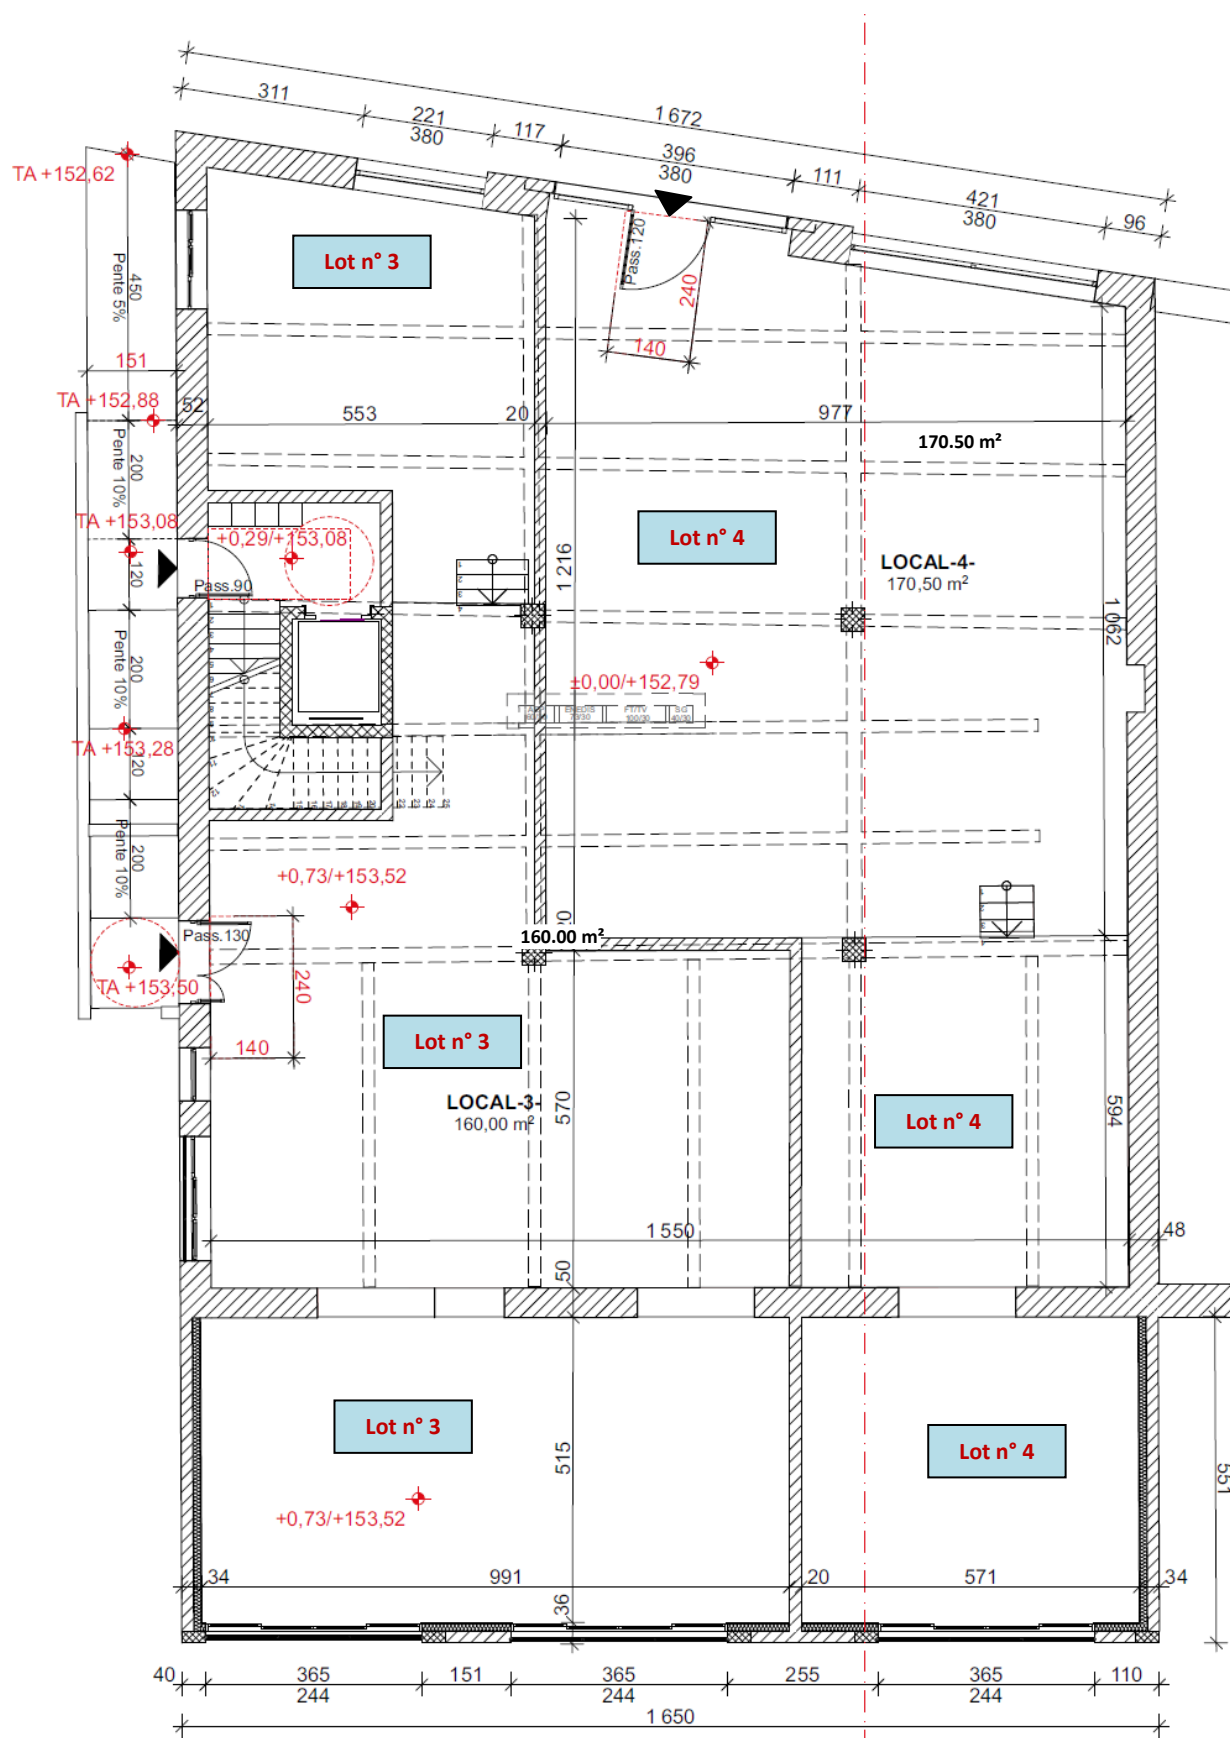

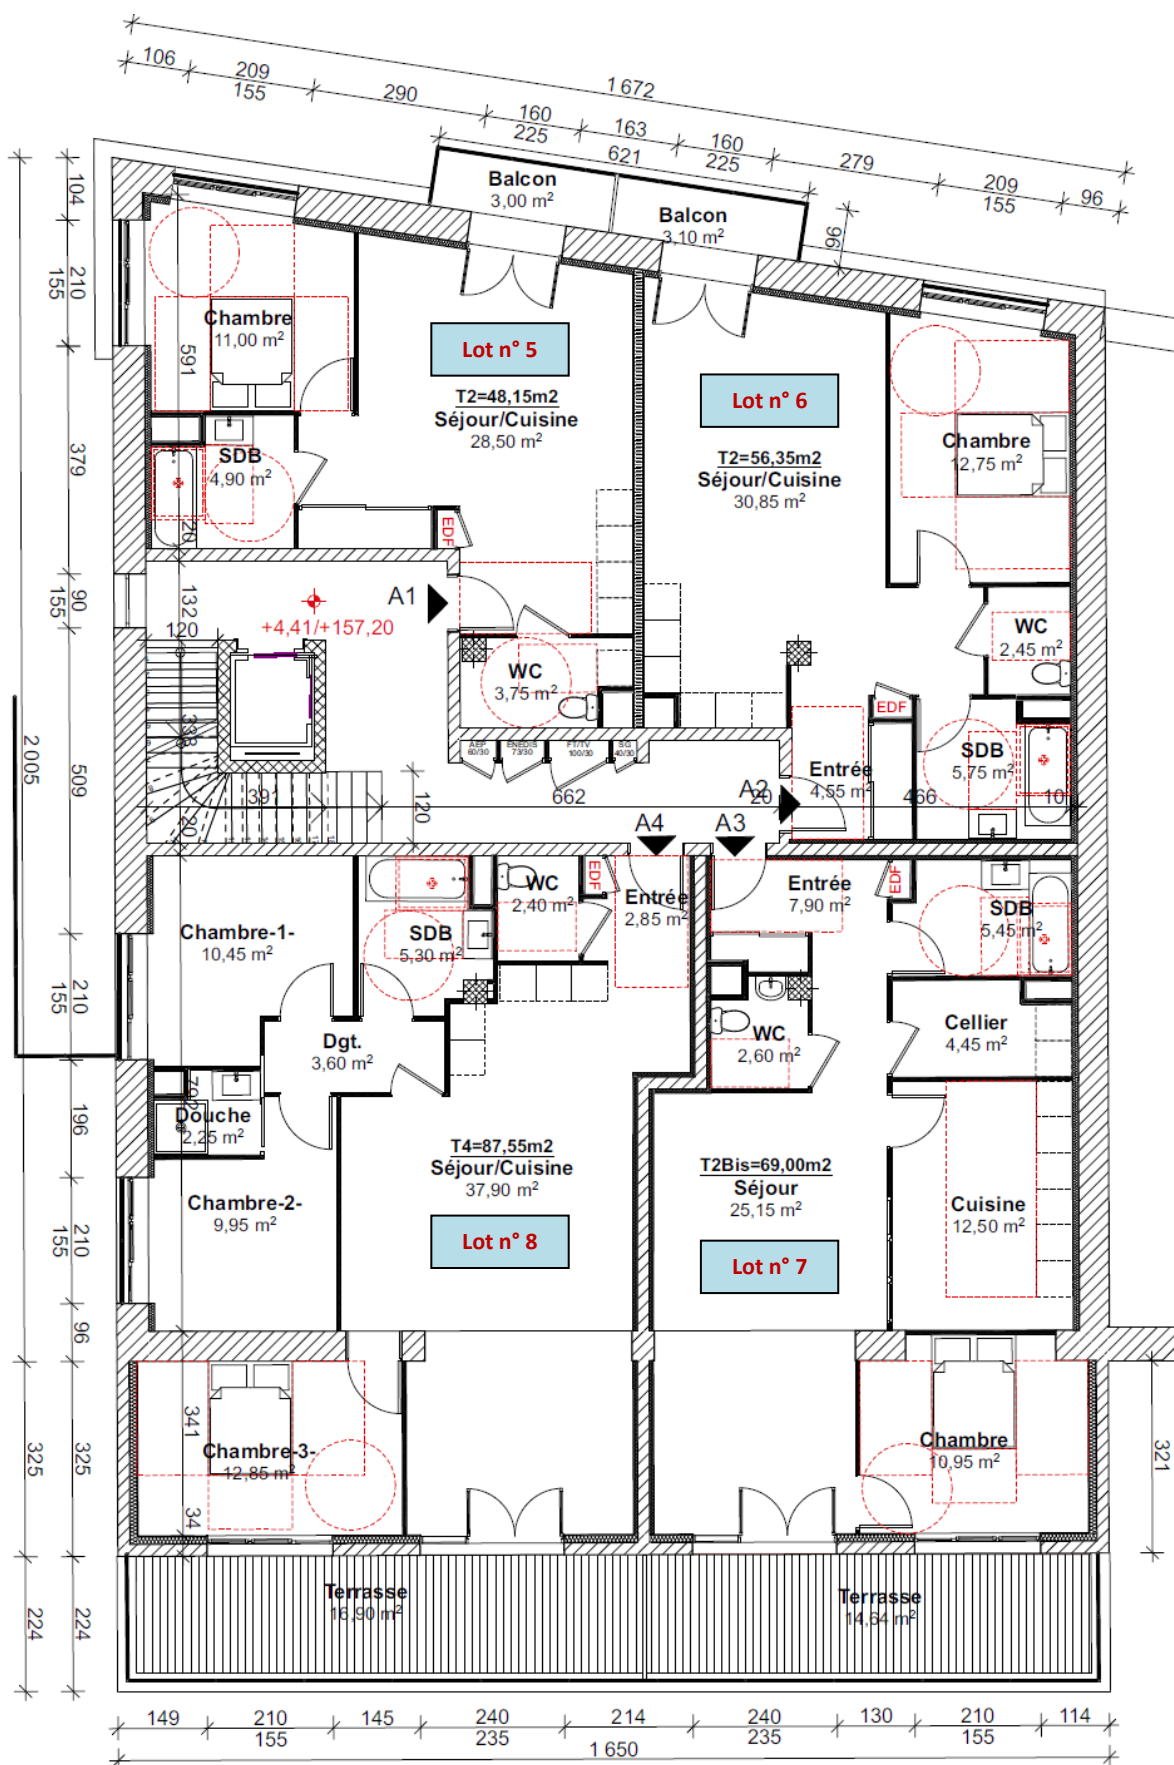
1^{er} étage - Bâtiment 1

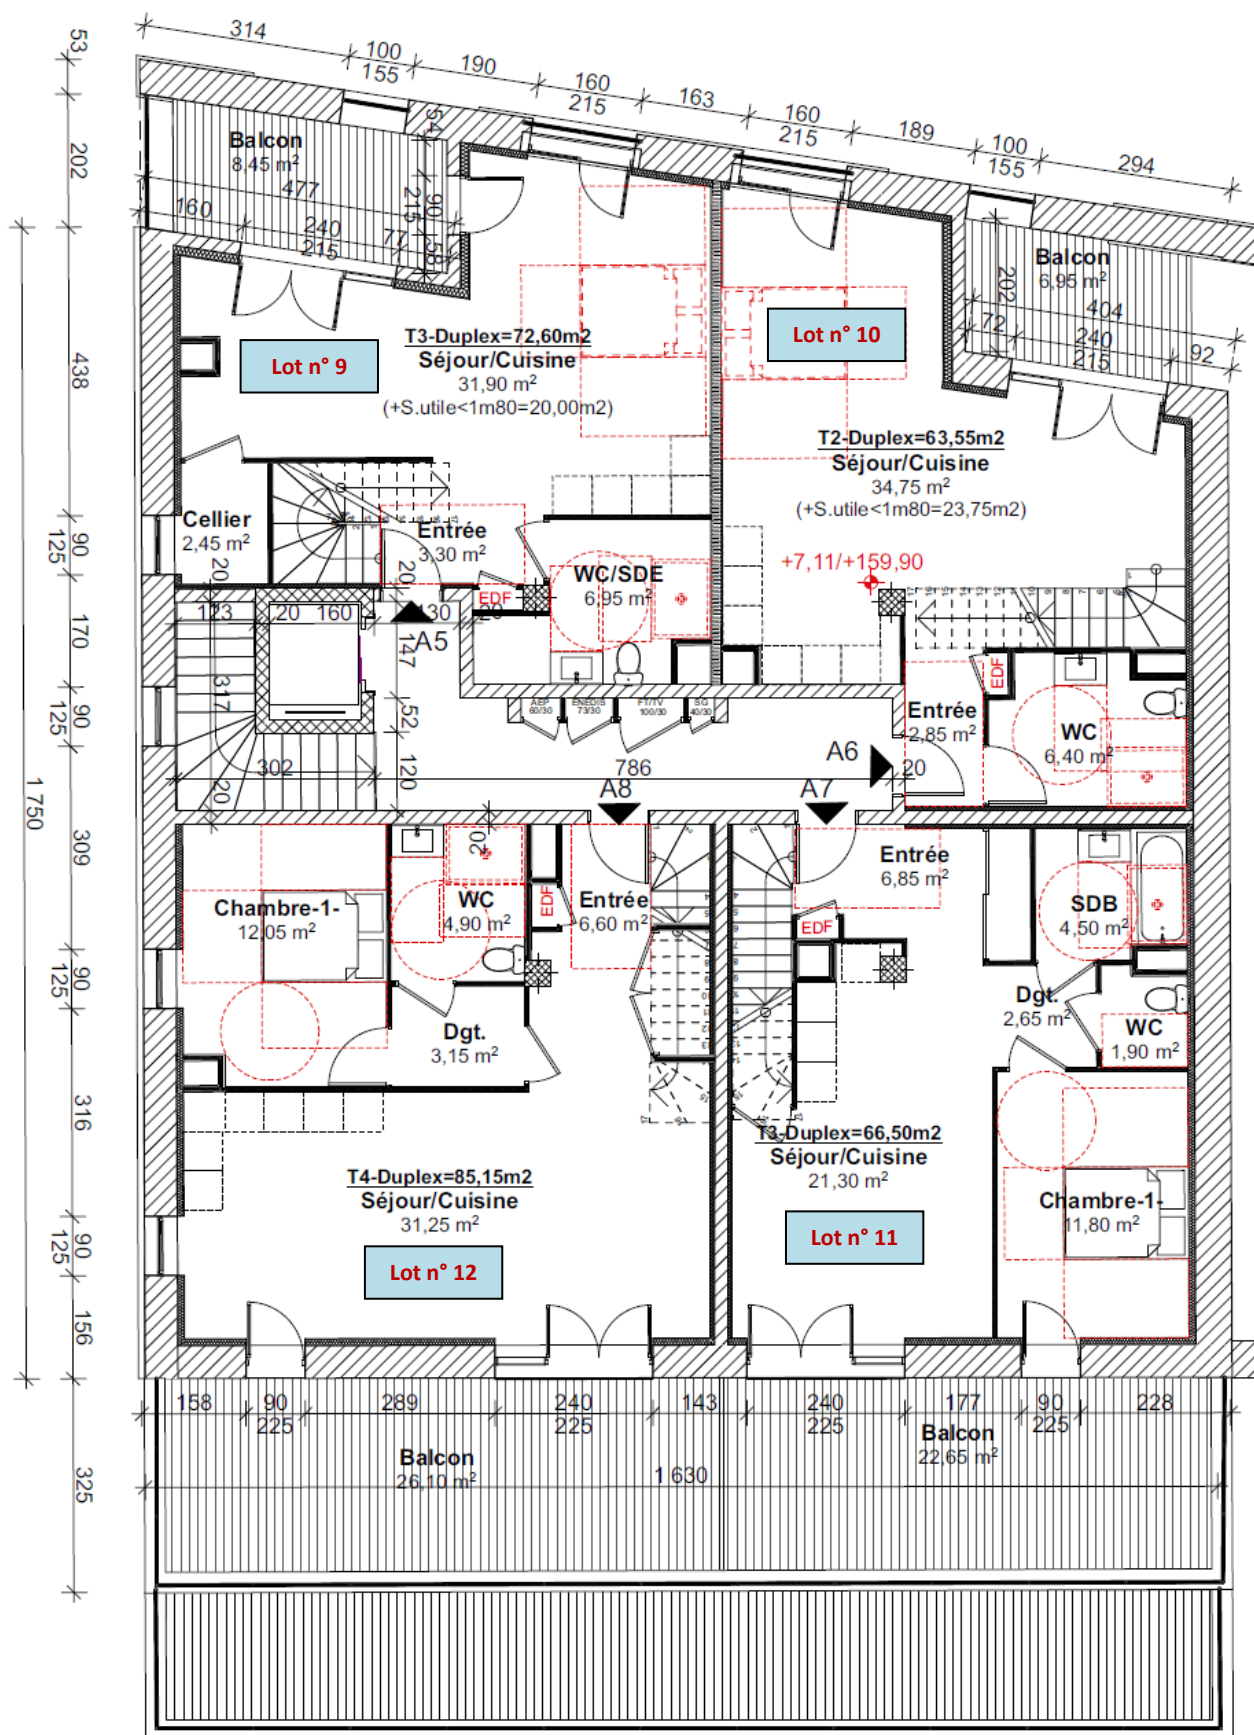2^{ème} étage - Bâtiment 1

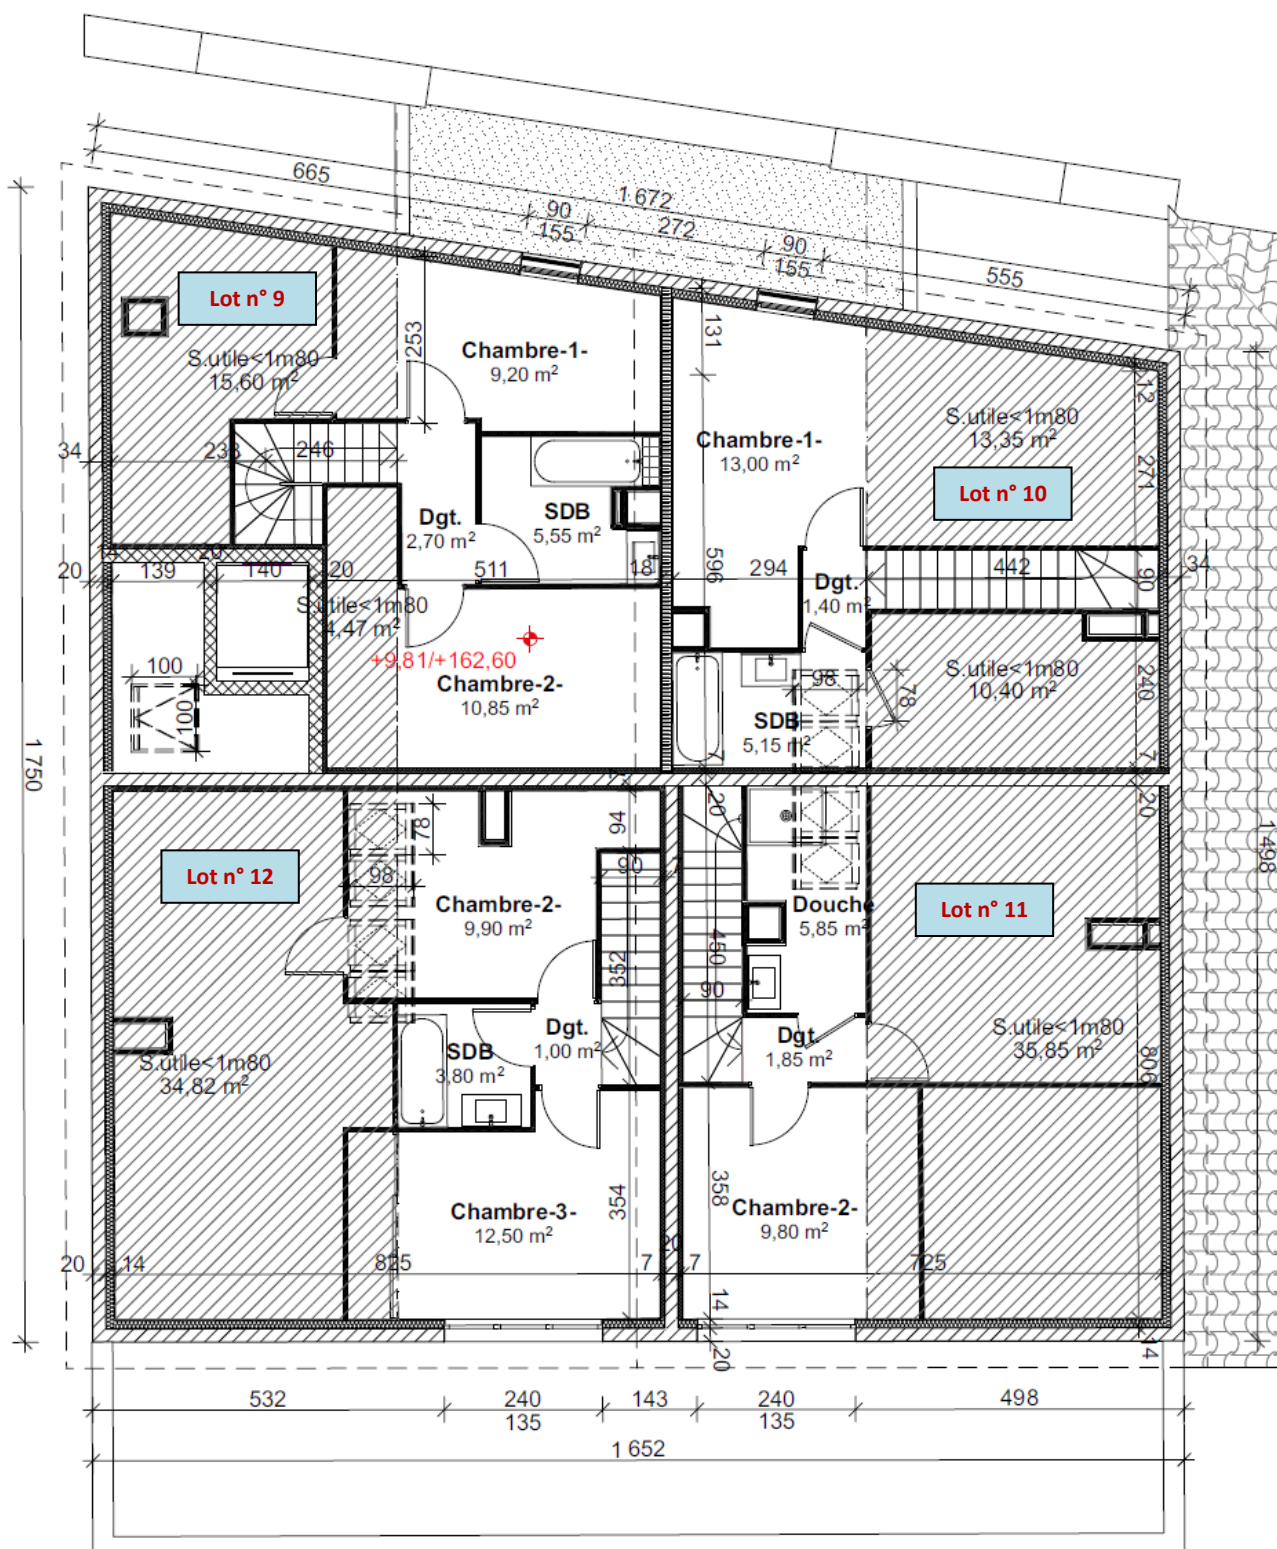3^{ème} étage - Bâtiment 1



Rez-de-jardin - Bâtiment 2

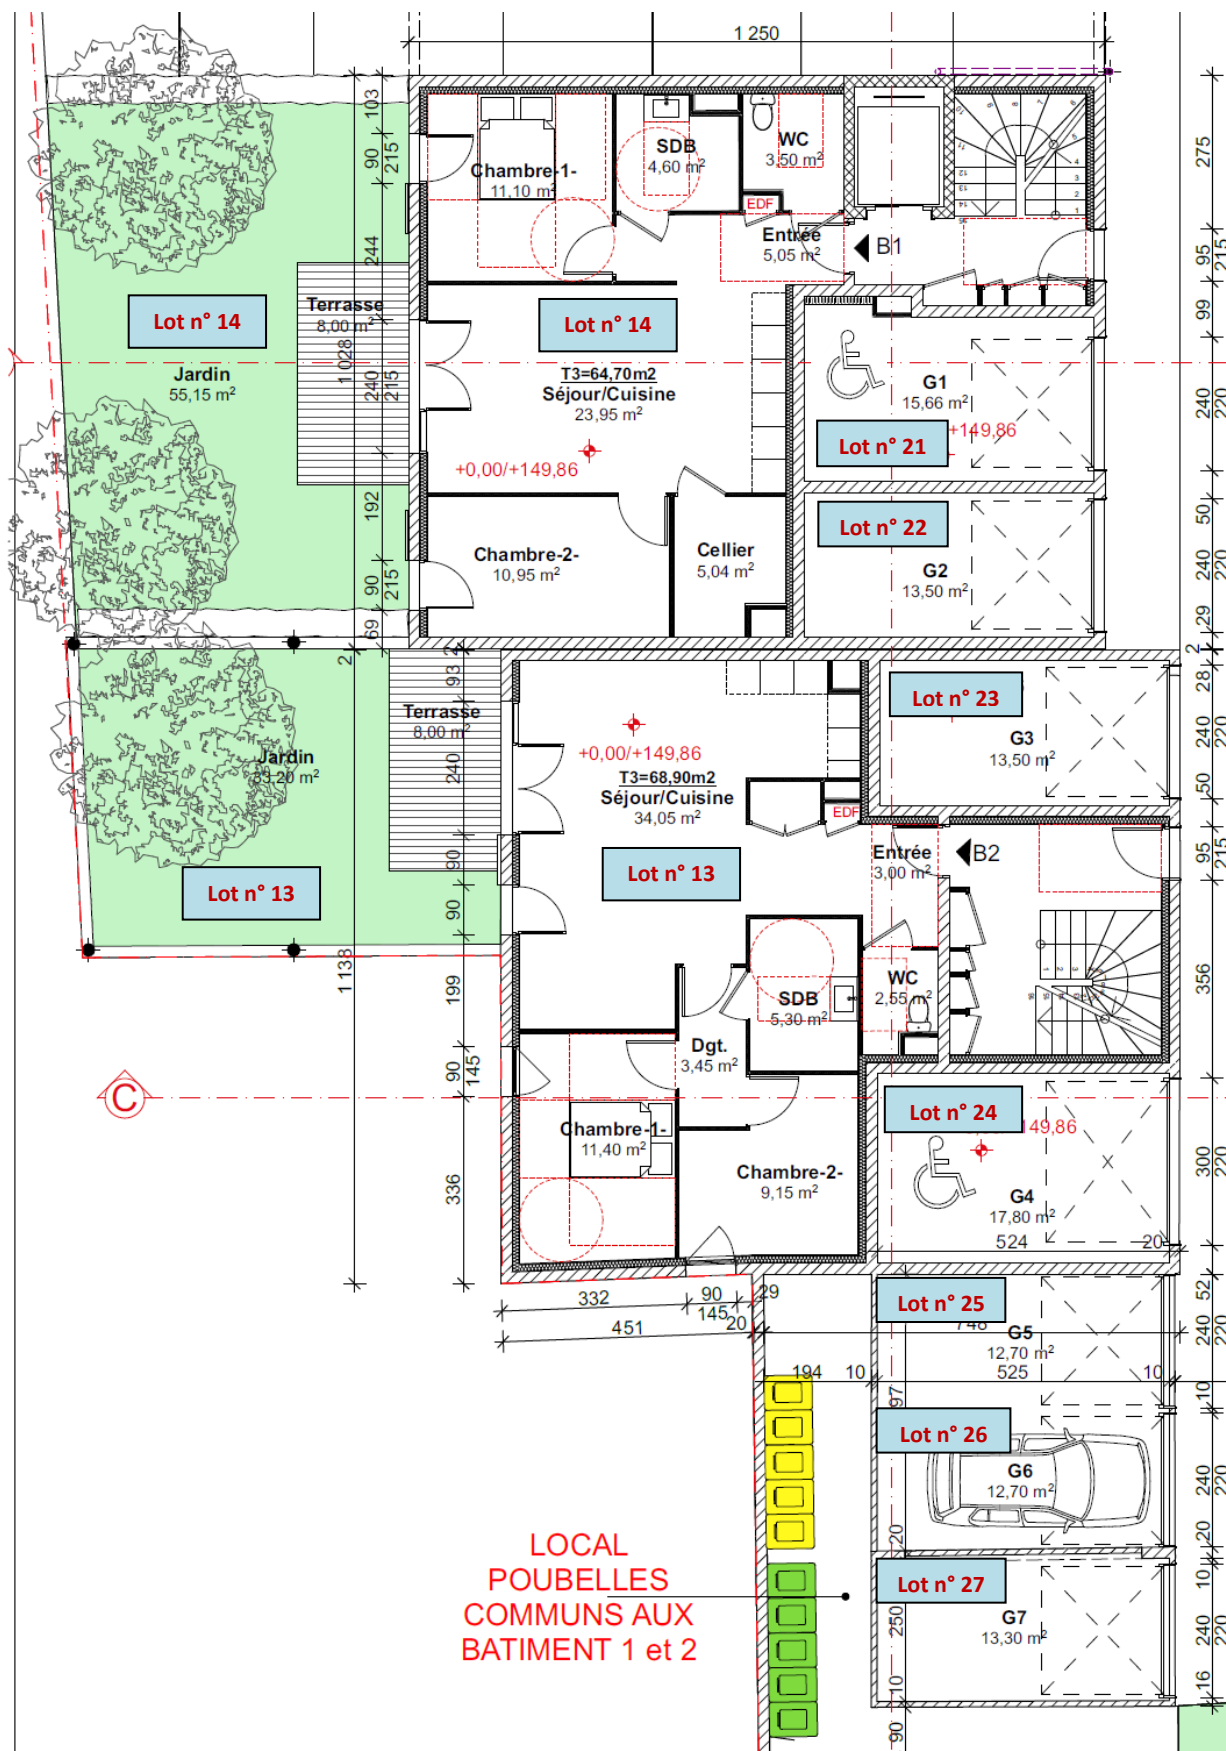


The architectural floor plan illustrates a three-story residential building with four distinct lots, each with its own set of rooms and dimensions. The plan is oriented with a north arrow pointing towards the top right. The building's overall dimensions are 160m by 1090m. The lots are labeled as follows:

- Lot n° 18 (Top):** T3=64,40m² Séjour/Cuisine 25,45 m². Rooms include Balcon (6,80 m²), SDB (4,70 m²), Dgt. (70 m²), WC (1,80 m²), Chambre-2 (13,25 m²), and Chambre-1 (17,50 m²). Stairs are located at B4 and B3.
- Lot n° 17 (Middle):** T3=67,30m² Séjour/Cuisine 24,20 m². Rooms include Balcon (5,35 m²), SDB (6,15 m²), Dgt. (1,70 m²), WC (2,15 m²), and Chambre-1 (12,25 m²). Stairs are located at B3 and B4.
- Lot n° 16 (Bottom Middle):** T5=100,65m² Séjour/Cuisine 30,60 m². Rooms include Balcon (4,85 m²), SDB/WC (6,45 m²), Dgt. (4,50 m²), WC (1,50 m²), and Chambre-1 (10,65 m²). Stairs are located at B6 and B5.
- Lot n° 15 (Bottom Right):** T5=112,75m² Séjour/Cuisine 29,10 m². Rooms include Balcon (30,25 m²), SDB (6,15 m²), Dgt. (1,70 m²), WC (2,15 m²), and Chambre-1 (12,25 m²). Stairs are located at B5 and B6.

The plan also shows common areas, stairs, and elevators. The building's overall dimensions are 160m by 1090m. The plan is oriented with a north arrow pointing towards the top right.

2^{ème} étage - Bâtiment 2

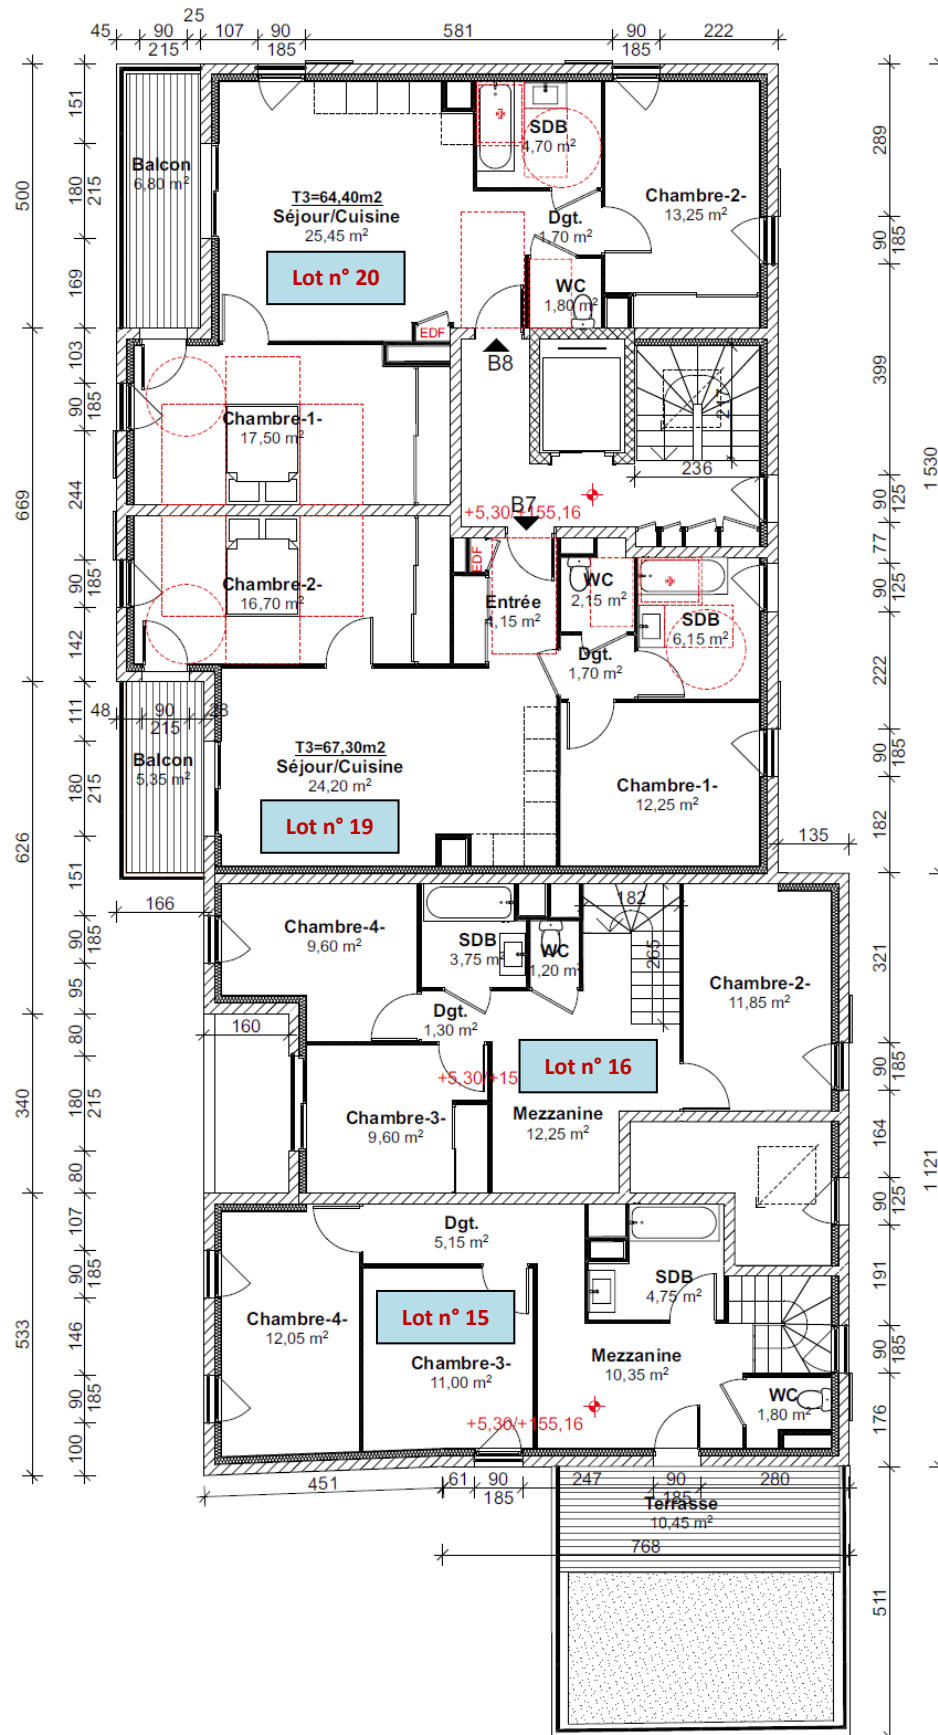


Mutuelle d'Assurance de la Ville de Thann

Société d'Assurance Mutuelle à cotisations variables
4 Rue de la Thur 68800 THANN – www.mavit-assurances.fr

Tél : 03 89 37 10 20 – contact@mavit.fr

Entreprise régie par le code des Assurances

MEMBRE DU GROUPE DES ASSURANCES MUTUELLES DE L'EST (GAMEST)

227 **VOTRE COURTIER :**
CABINET DIAGNOS
VILLAEYS OLIVIER
14 RUE DU MARECHAL DE LATTRE
DE TASSIGNY
67170 BRUMATH
N° Orias : 07031035
Contact@diagnos.fr

ATTESTATION D'ASSURANCE RESPONSABILITE CIVILE PROFESSIONNELLE

La société MAVIT atteste que l'entreprise

FPE EXPERTISE

189 CHEMIN DES GRANDES BRUYERES 38121 CHONAS L AMBALLAN

a souscrit un contrat d'assurance : POLICE n° 2011852

couvrant les conséquences générales et particulières de sa Responsabilité Civile Professionnelle suivant les dispositions des conditions générales DGRCPDI 10.20 et particulières.

Montant des garanties réglementaires 300 000 € par sinistre et 500 000 € par an.

Audit énergétique

Diagnostic Amiante

- examen avant vente ou location
- Diagnostic Technique Amiante (DTA) dont ascenseur
- avant travaux, après travaux, avant démolition
- vérification périodique de l'état de conservation des matériaux

Diagnostic Assainissement autonome ou collectif

Diagnostic Eco Prêt

Diagnostic Etat des Risques et Pollutions (ERP)

Diagnostic Etat de l'Installation Electrique dont télétravail

Diagnostic Etat de l'Installation Gaz

Diagnostic Etat des lieux (dont livraison de bien neuf)

Diagnostic Etat Parasitaire (Mérule, Insectes Xylophages, Champignons)

Diagnostic Loi Boutin

Diagnostic Loi Carrez

Diagnostic Millièmes

Diagnostic Performance Energétique (DPE)

Diagnostic Plomb (CREP, DRIP, Avant travaux, Plomb dans l'eau)

Diagnostic Termites

Calcul Réglementaire RT2005, RT2012, RE2020

Expertise en Valeur Vénale

Les garanties sont acquises à l'assuré sous réserve qu'il puisse justifier de toute l'expérience, qualification ou certification en vigueur, nécessaire à l'exercice de ses activités.

La présente attestation est délivrée pour servir et valoir ce que de droit. Elle vaut présomption simple d'assurance et ne peut notamment engager la Société d'Assurance en dehors des limites, clauses et conditions prévues au contrat auquel elle se réfère.

Elle est valable du 01/01/2023 au 31/12/2023 sous réserve du paiement de la cotisation.